




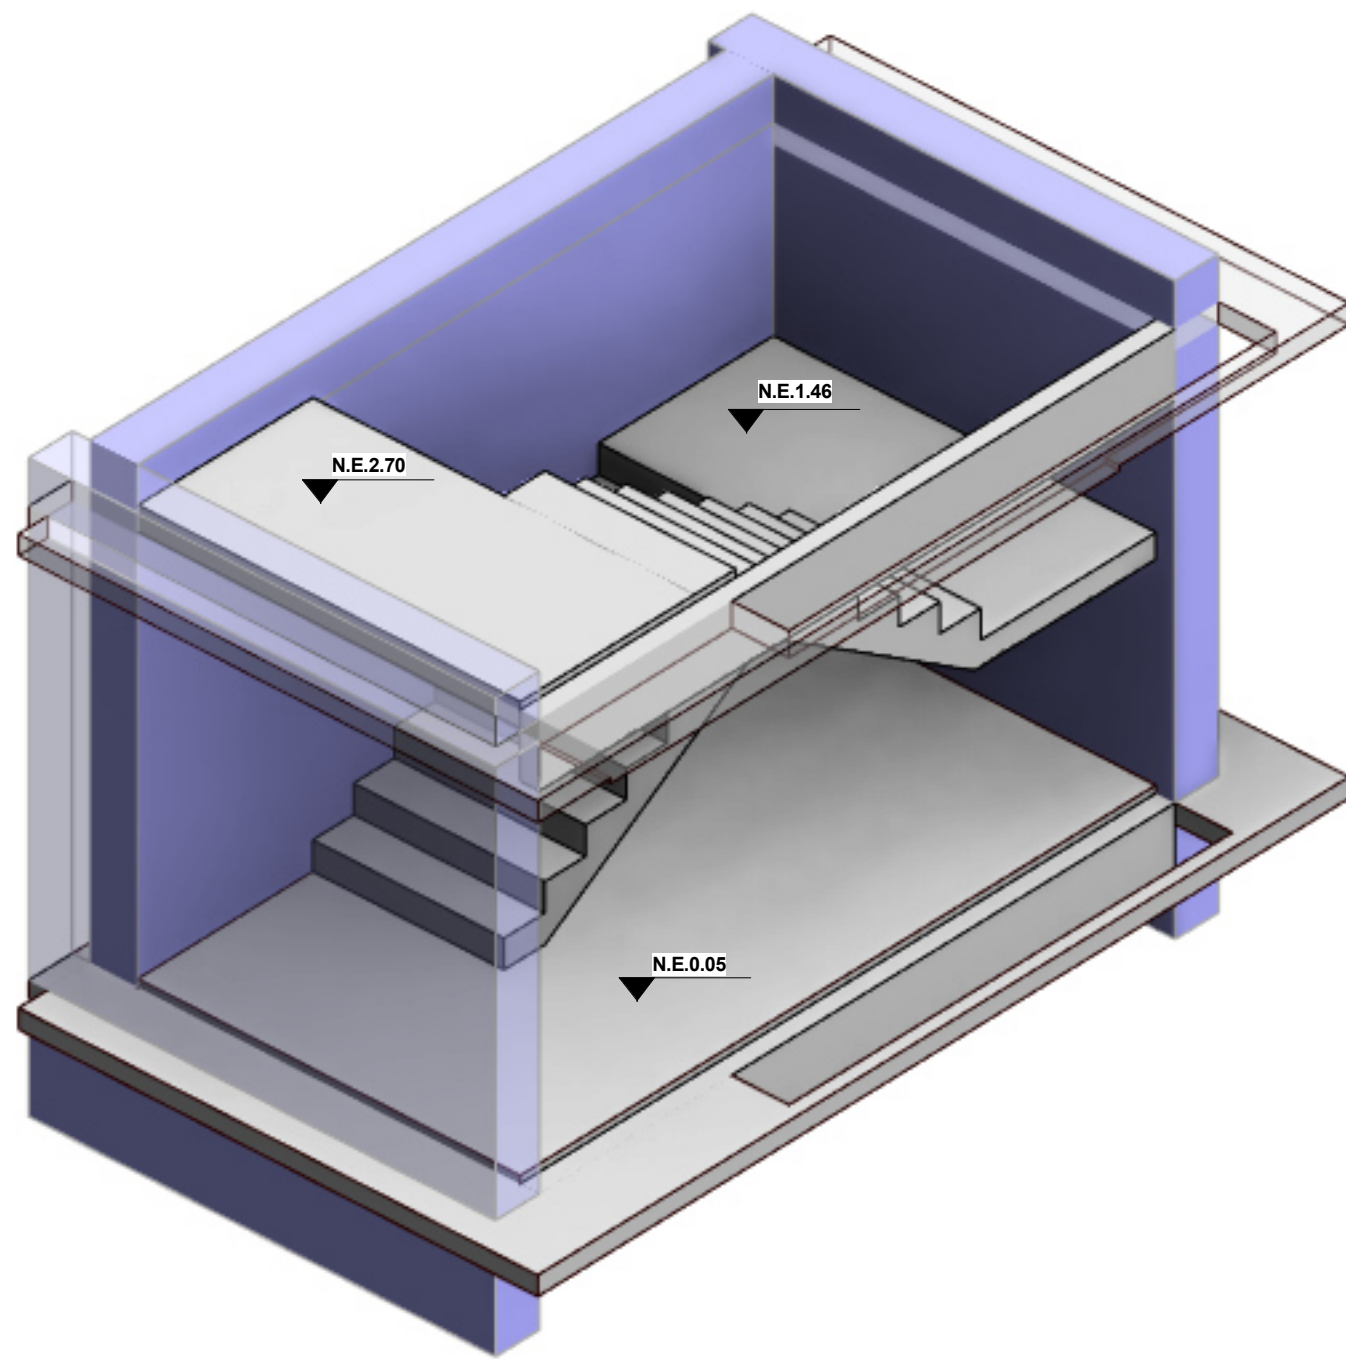


3D ESCALERA TIPO 1 DE PISO 1 A PISO 2
Sin escala

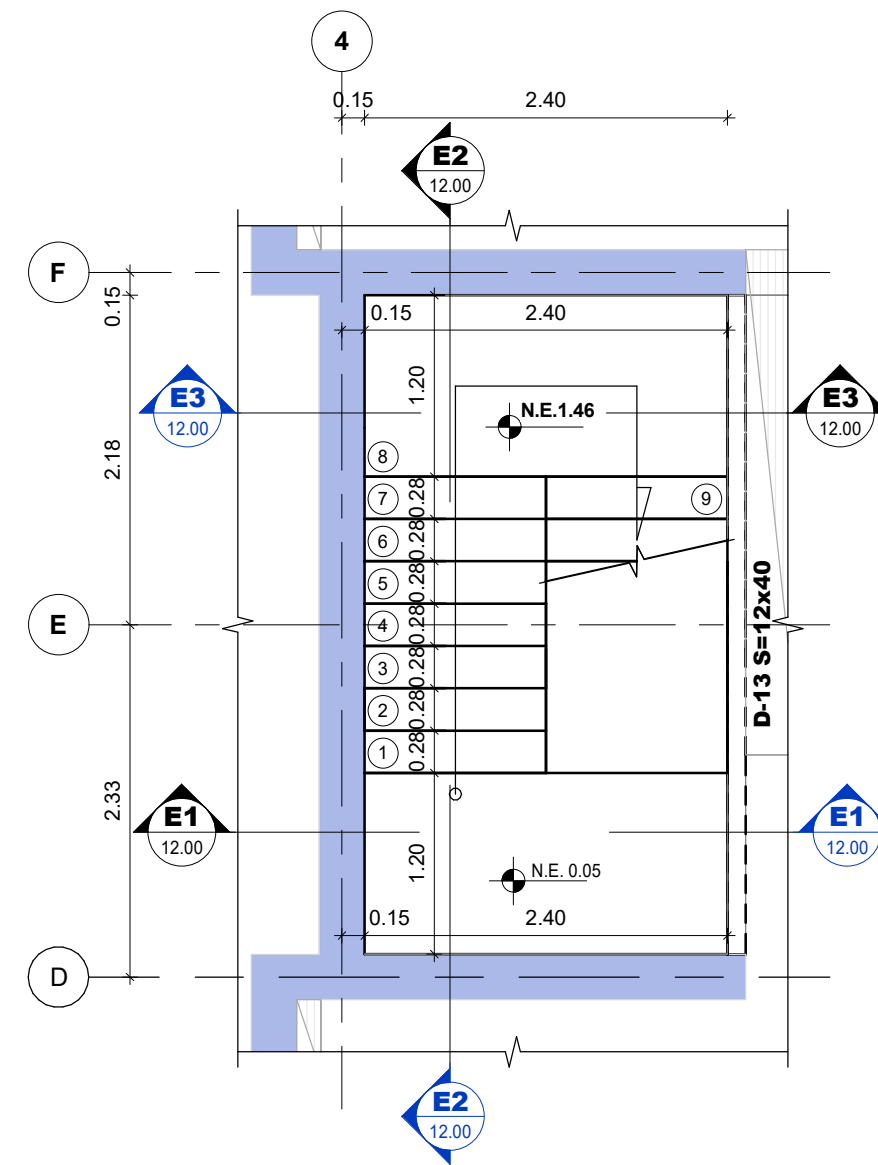


PLANTA ARRANQUE ESCALERA TIPO 1 (PISO 1 A 2)
Escala 1 : 50

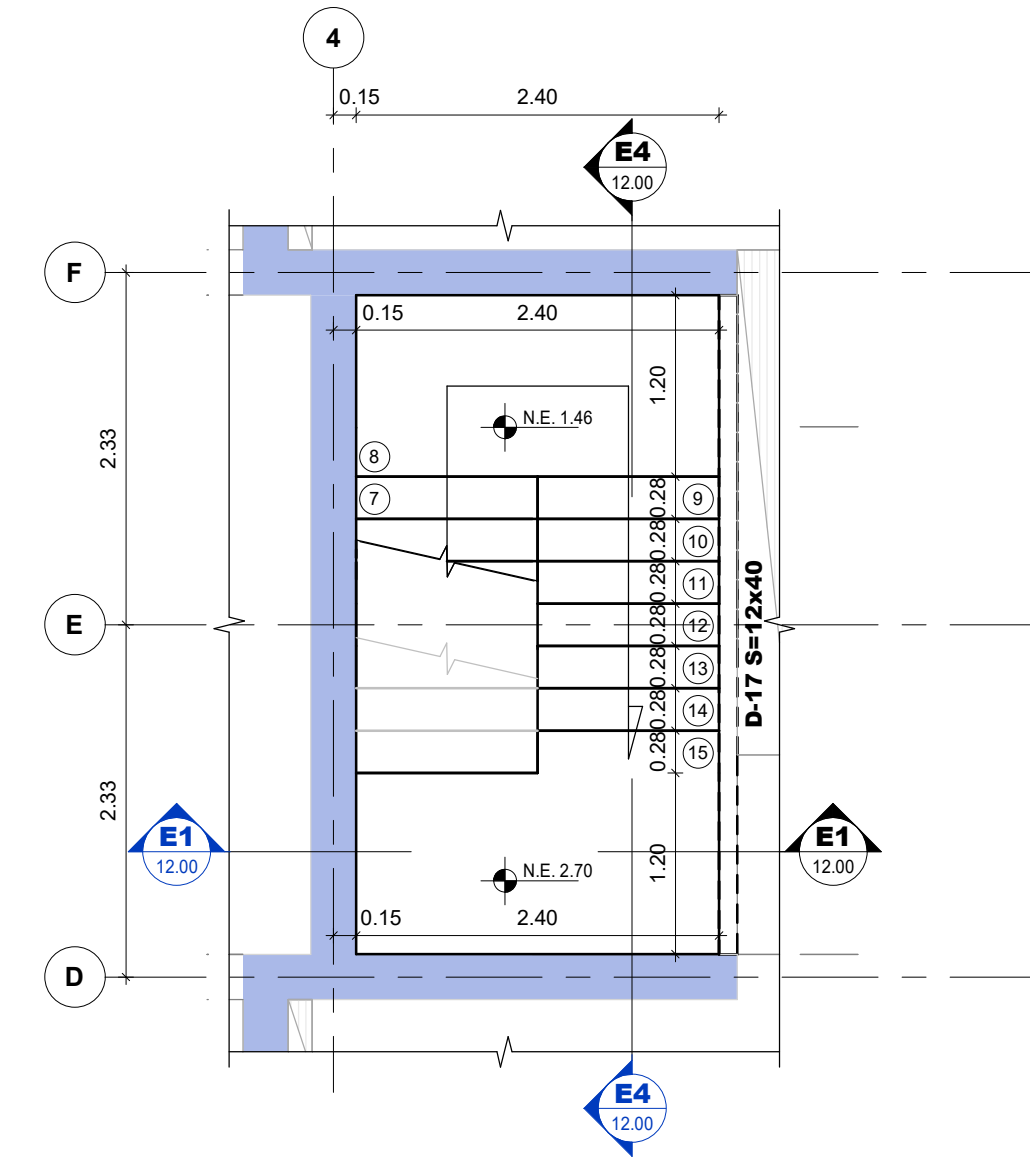

PLANTA LLEGADA ESCALERA TIPO 1 (PISO 1 A 2)
Escala 1 : 50

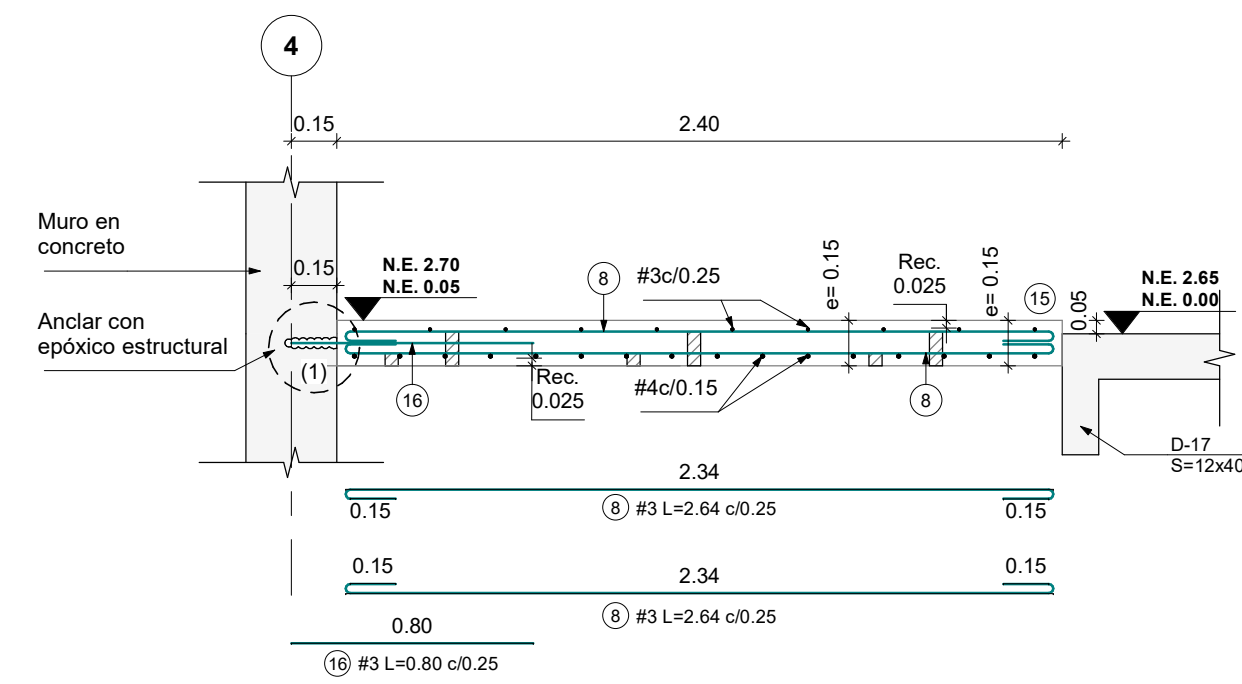


CORTE E-1
Escala 1 : 25

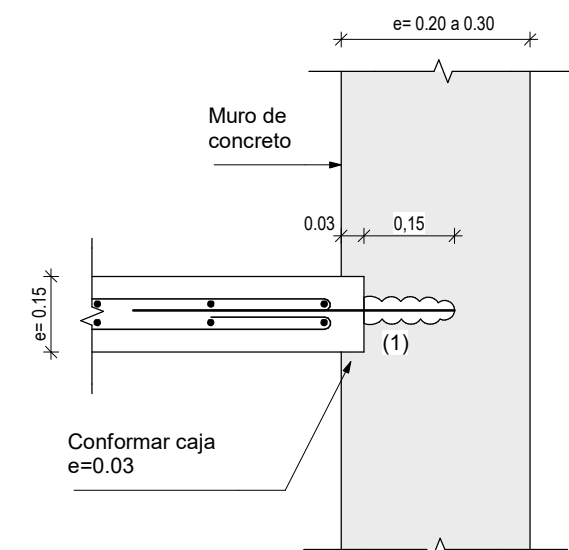


(1) Indica anclar con epóxico estructural


DETALLE 1
Escala 1 : 10

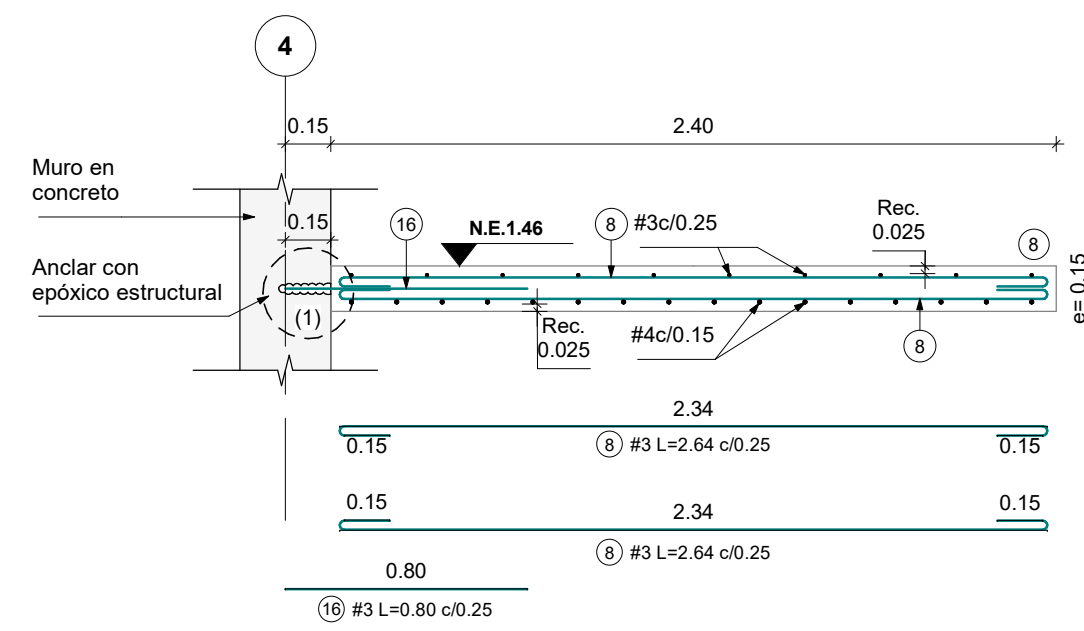

CORTE E-3
Escala 1 : 25

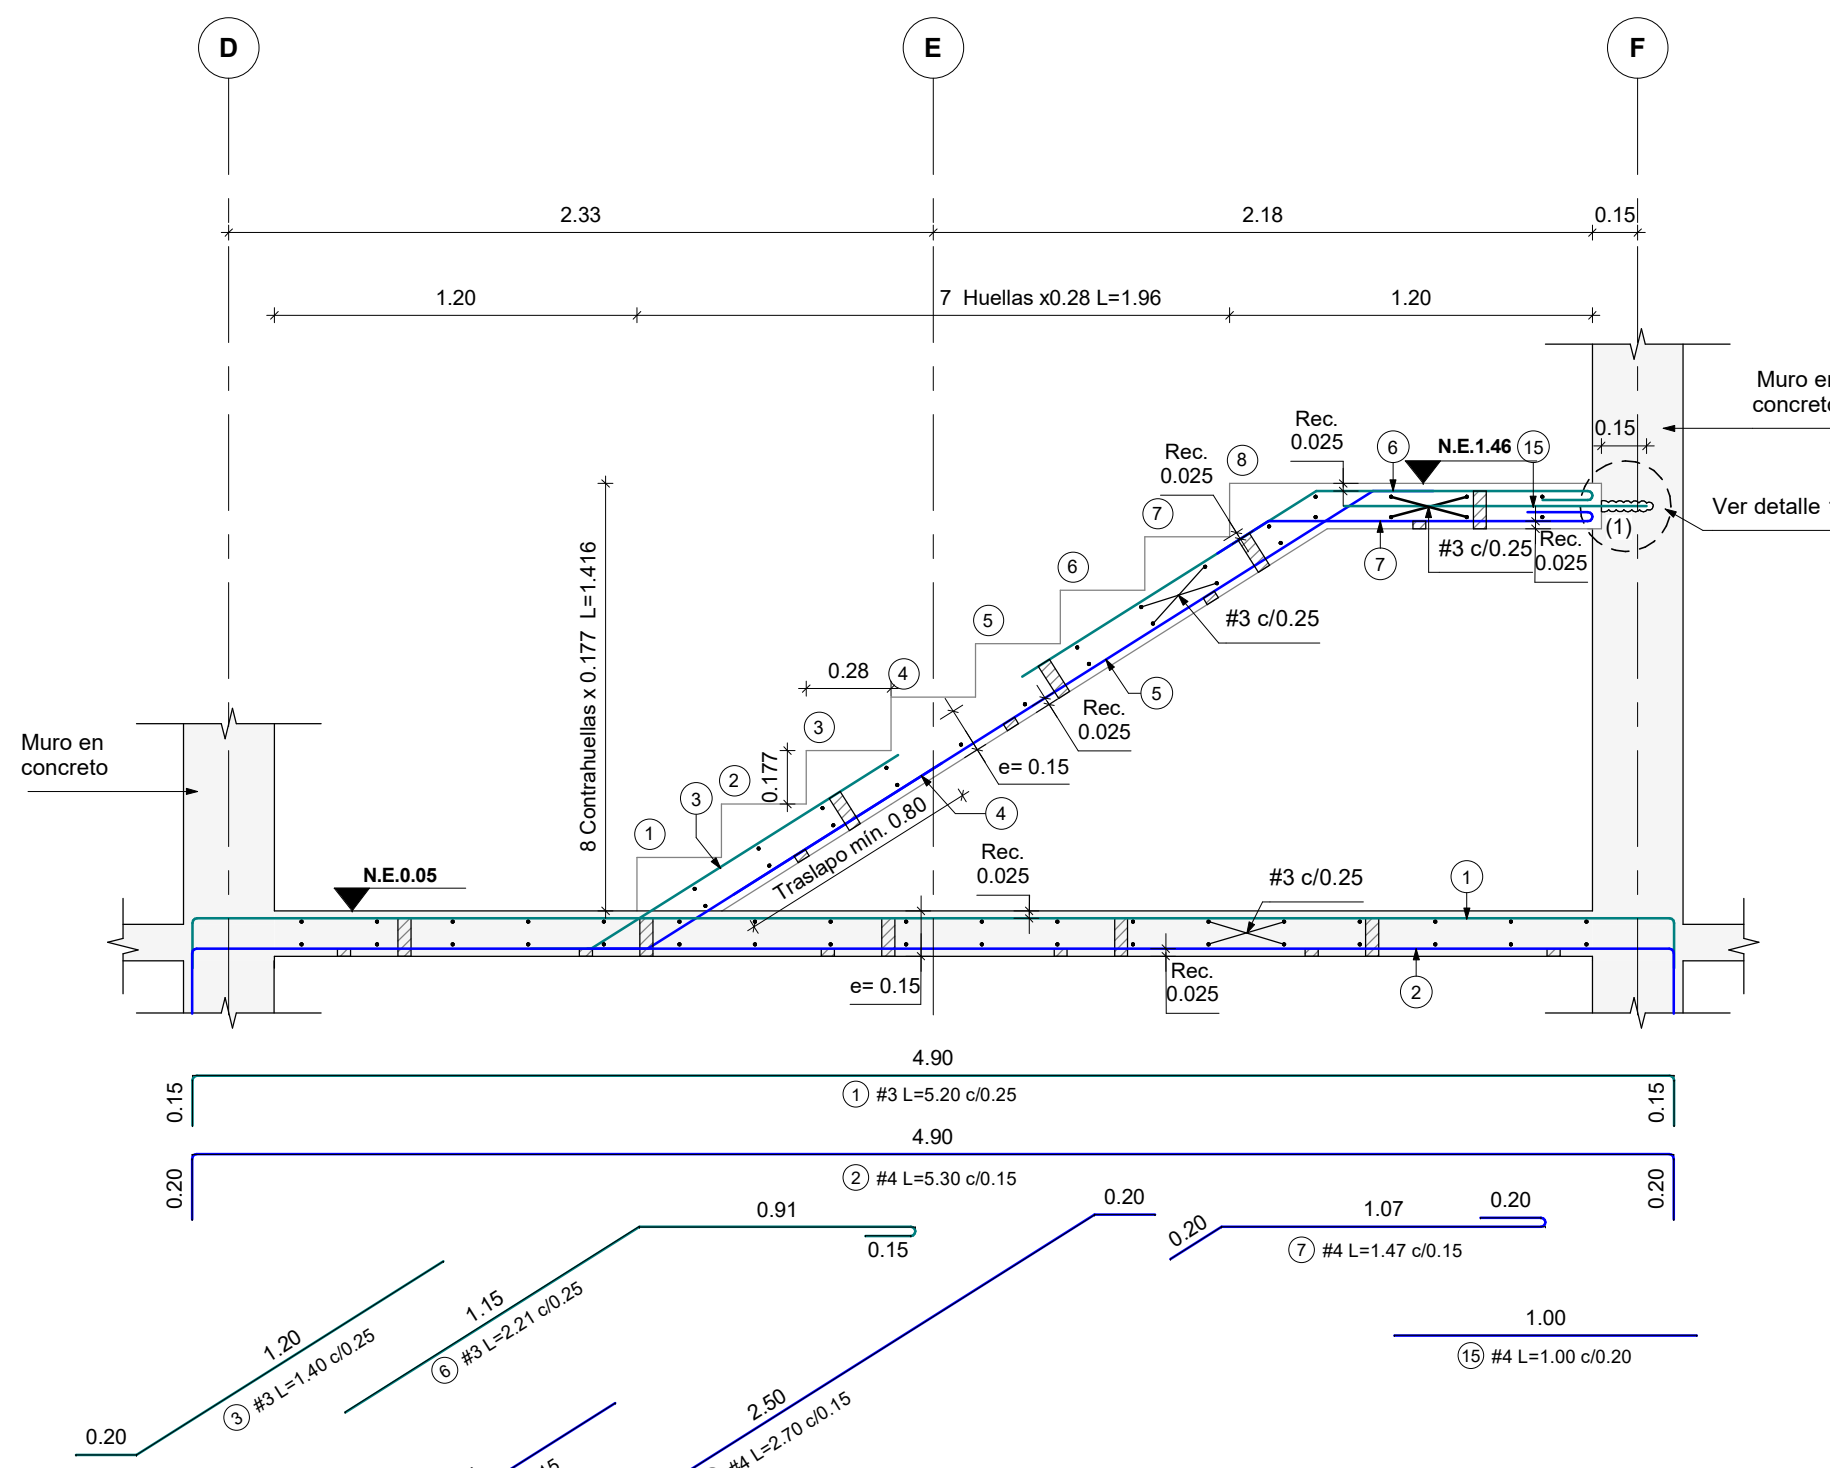

CORTE E-2
Escala 1 : 25

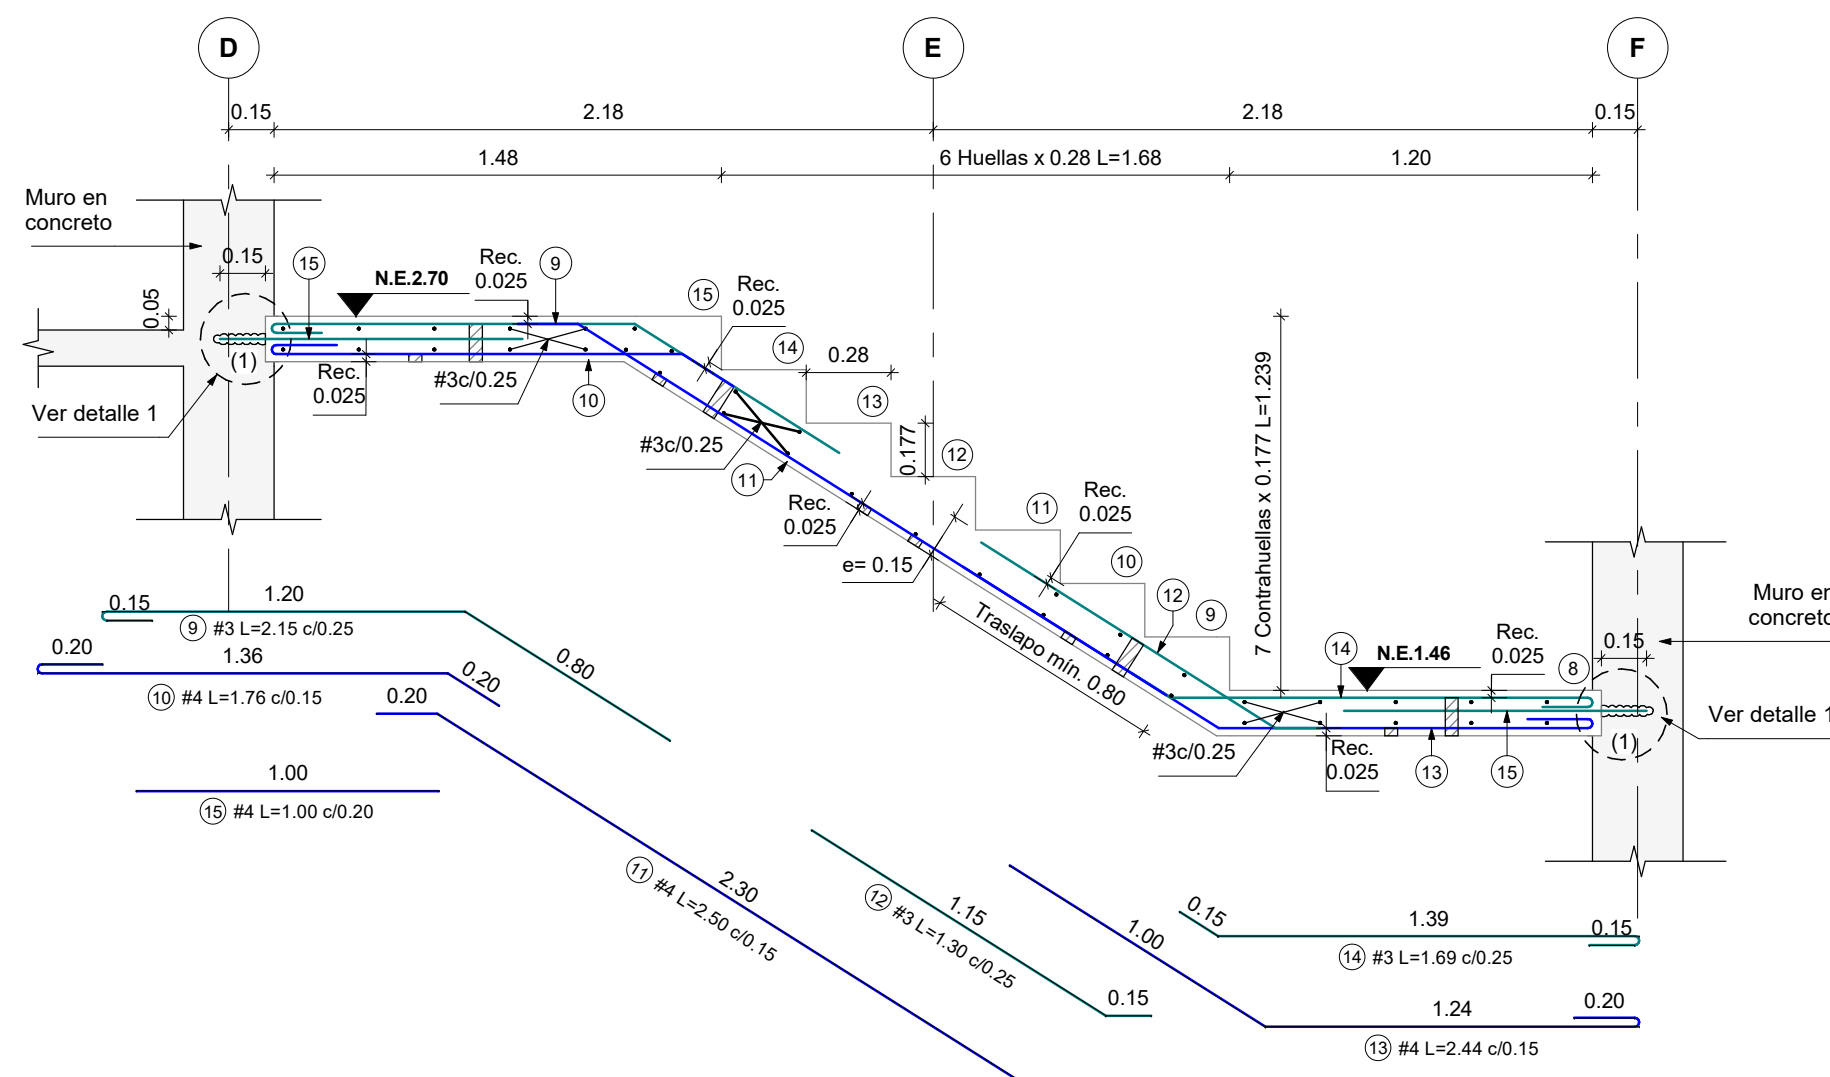

CORTE E-4
Escala 1 : 25

CONCRETO:
f_c=21 MPa
f_c=210 kg/cm²
f_c=3000 psi

NOTAS:
1. Ver detalles generales en PL N° 01.02

PLANO N° 12.00

VERSIÓN: 2

Aycardi Estructural

GERENTE DE PROYECTO
ROBERTO AYCARDI F.
MAT. 2520257258 CND

INGENIERO
CARLOS ANDRÉS WILCHES C.

MODELADOR
DANIEL CASTELLANOS

MODIFICACIONES	FECHA
Emisión Inicial	21-03-2025
Ajuste presentación	26-02-2026



LA SCALA

LA SCALA_EST_TOR-1

TORRE 1

CALLE 170 CON AV. BOYACA

DESPIECE ESCALERA TIPO 1 (PISO 1 A 2)

LA SCALA_EST_TOR-1_12.00_ESC-2

REVISOR ESTRUCTURAL
RAMÓN ANDRÉS ALVAREZ MANTILLA
MAT. 25202-346546 CND.

PLANO N°

VERSIÓN:

12.00

2

