



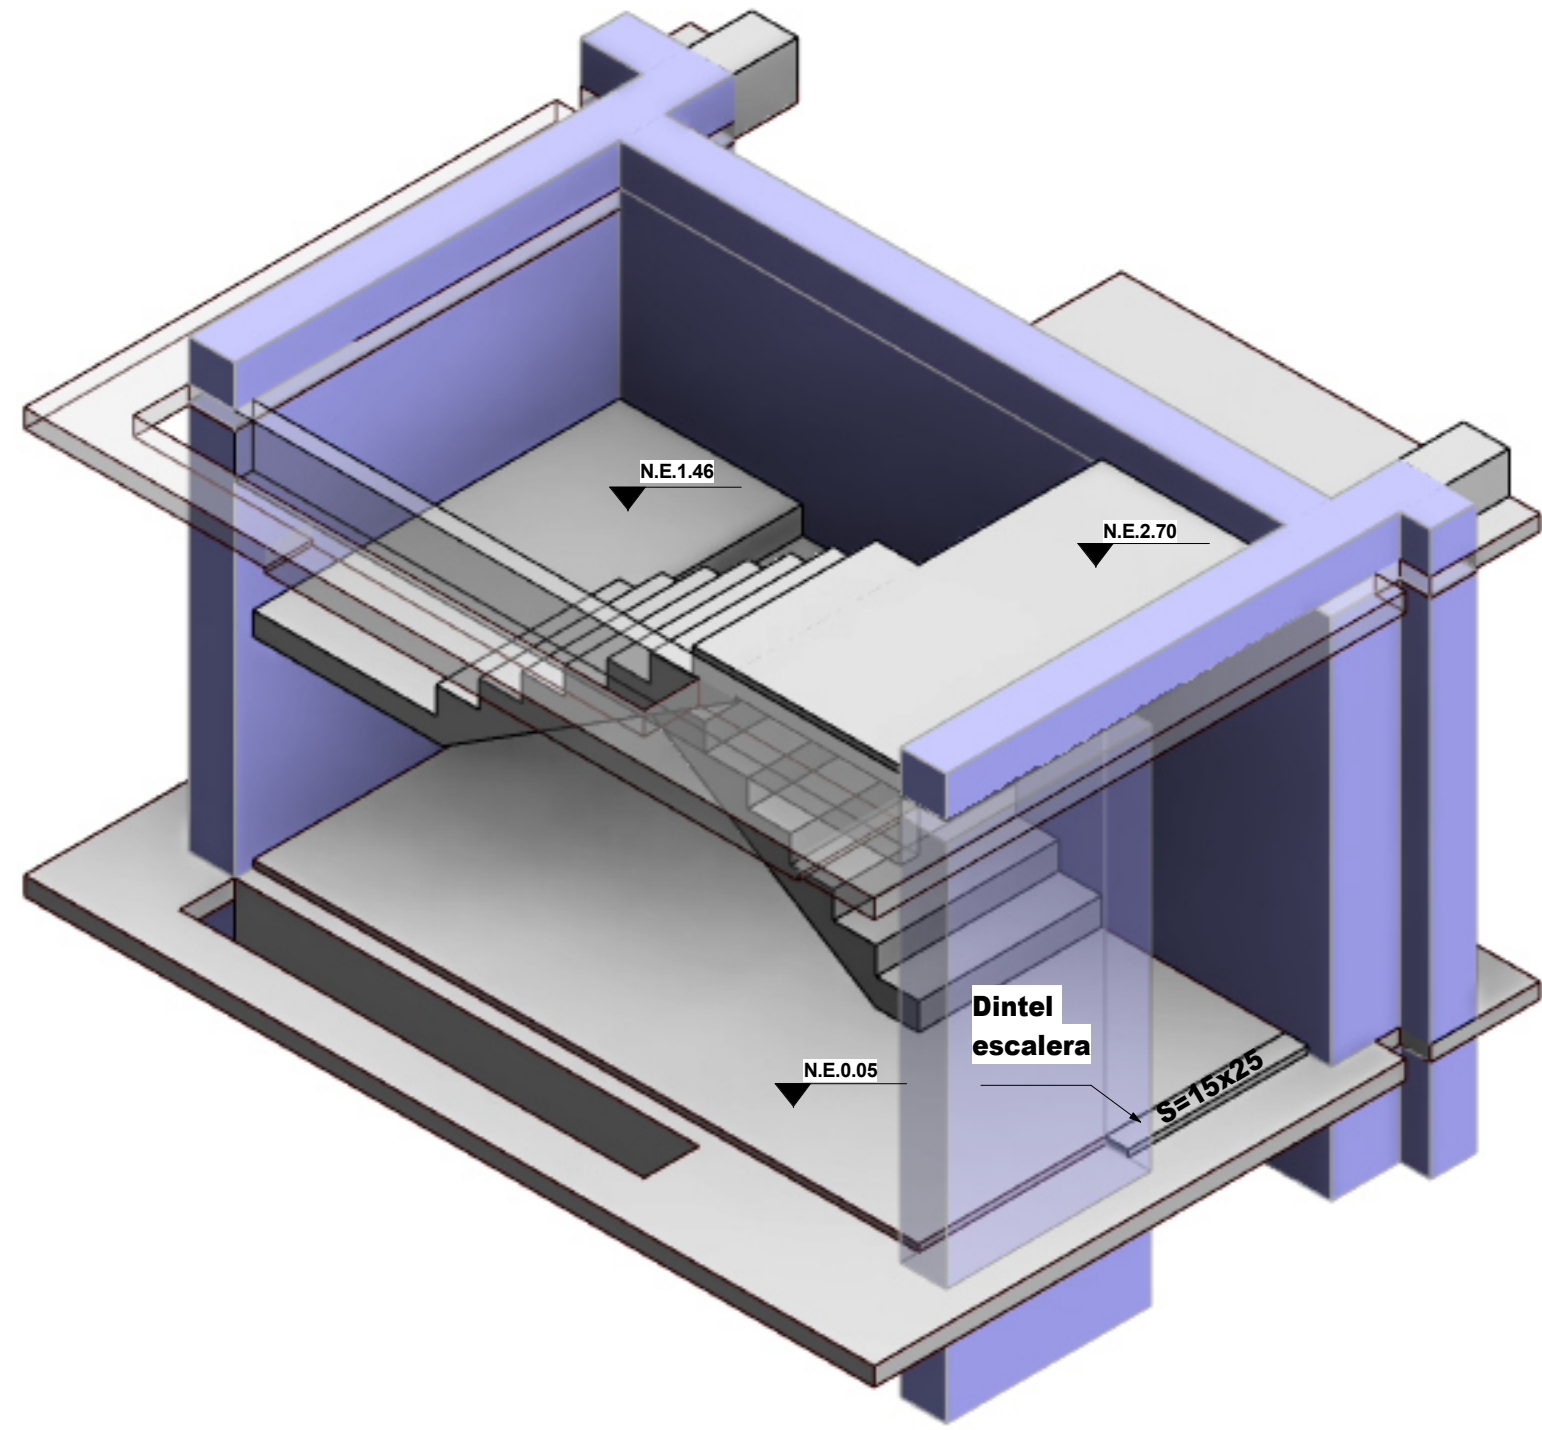


3D ESCALERA TIPO 2 DE PISO 1 A PISO 2
Sin escala

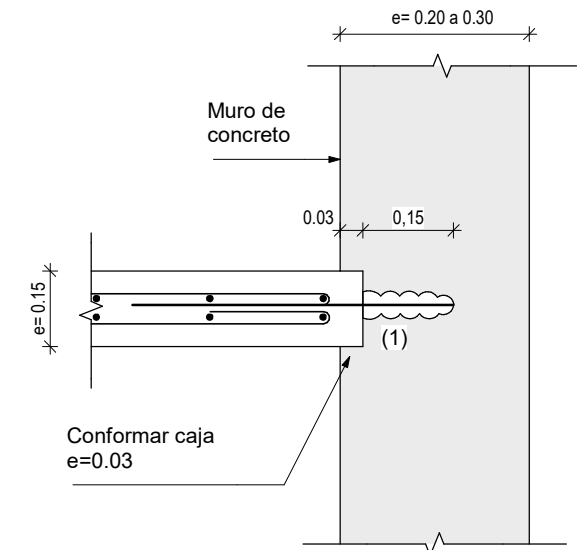


(1) Indica anclar con epóxico estructural


DETALLE 1
Escala 1 : 10

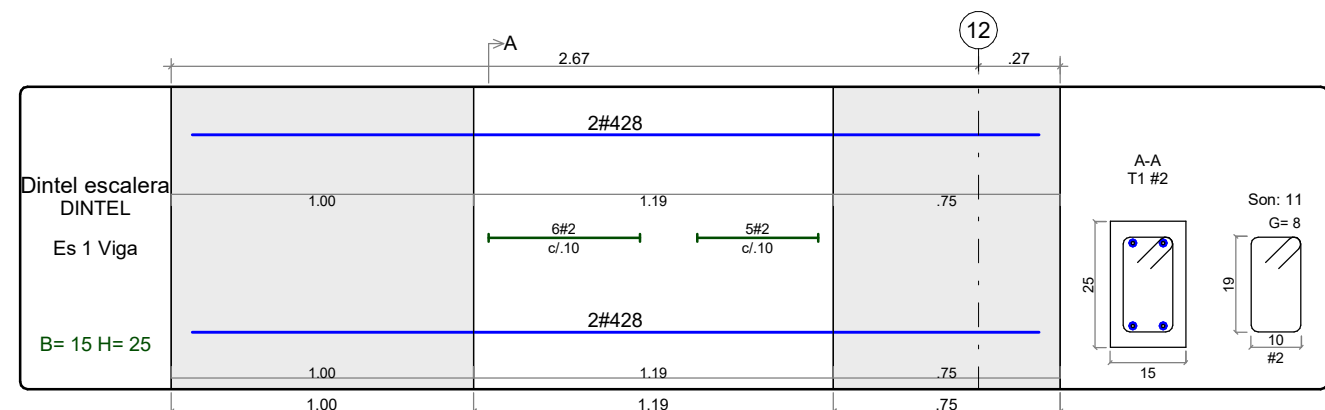


DESPIECE DINTTEL ESCALERA
Escala 1 : 25

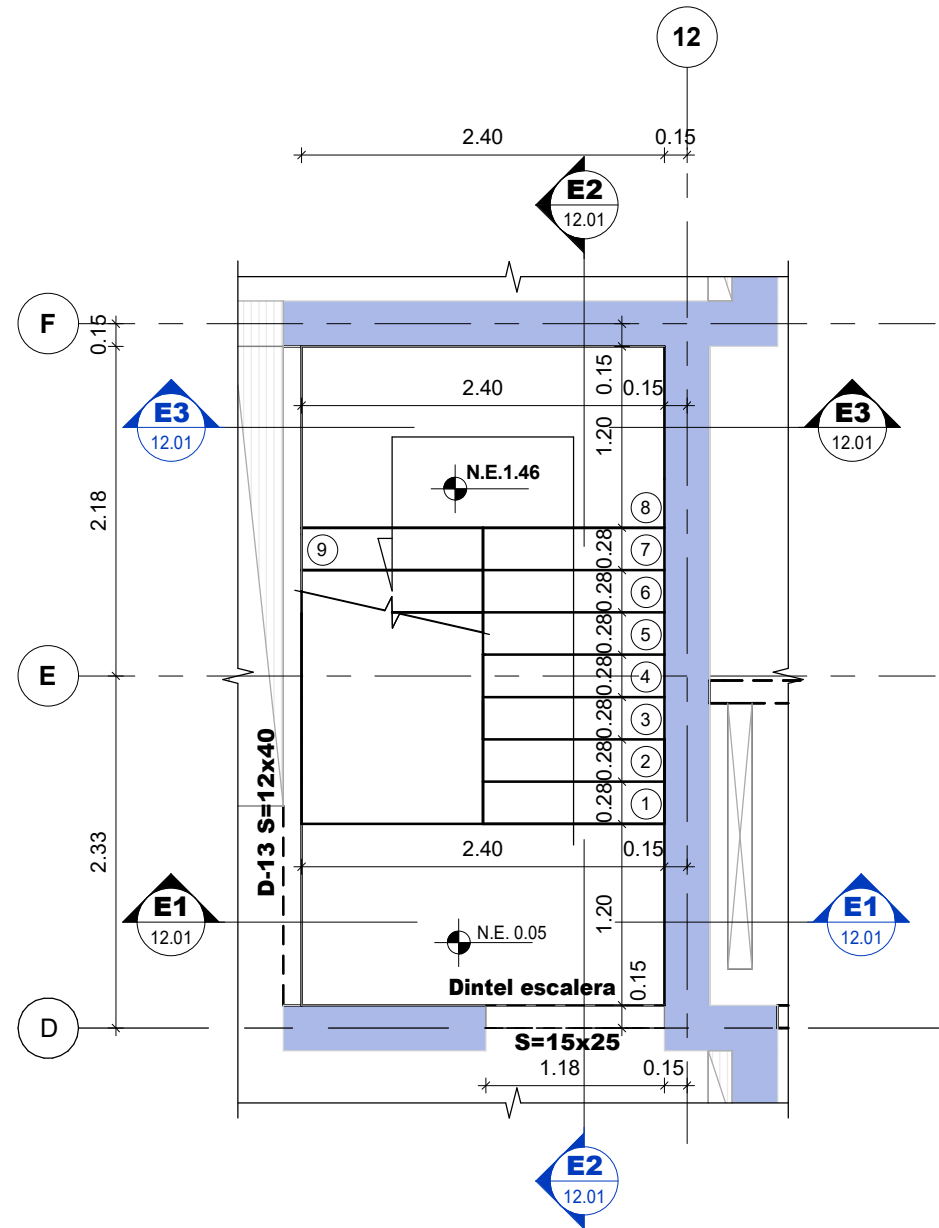


PLANTA ARRANQUE ESCALERA TIPO 2 (PISO 1 A 2)
Escala 1 : 50

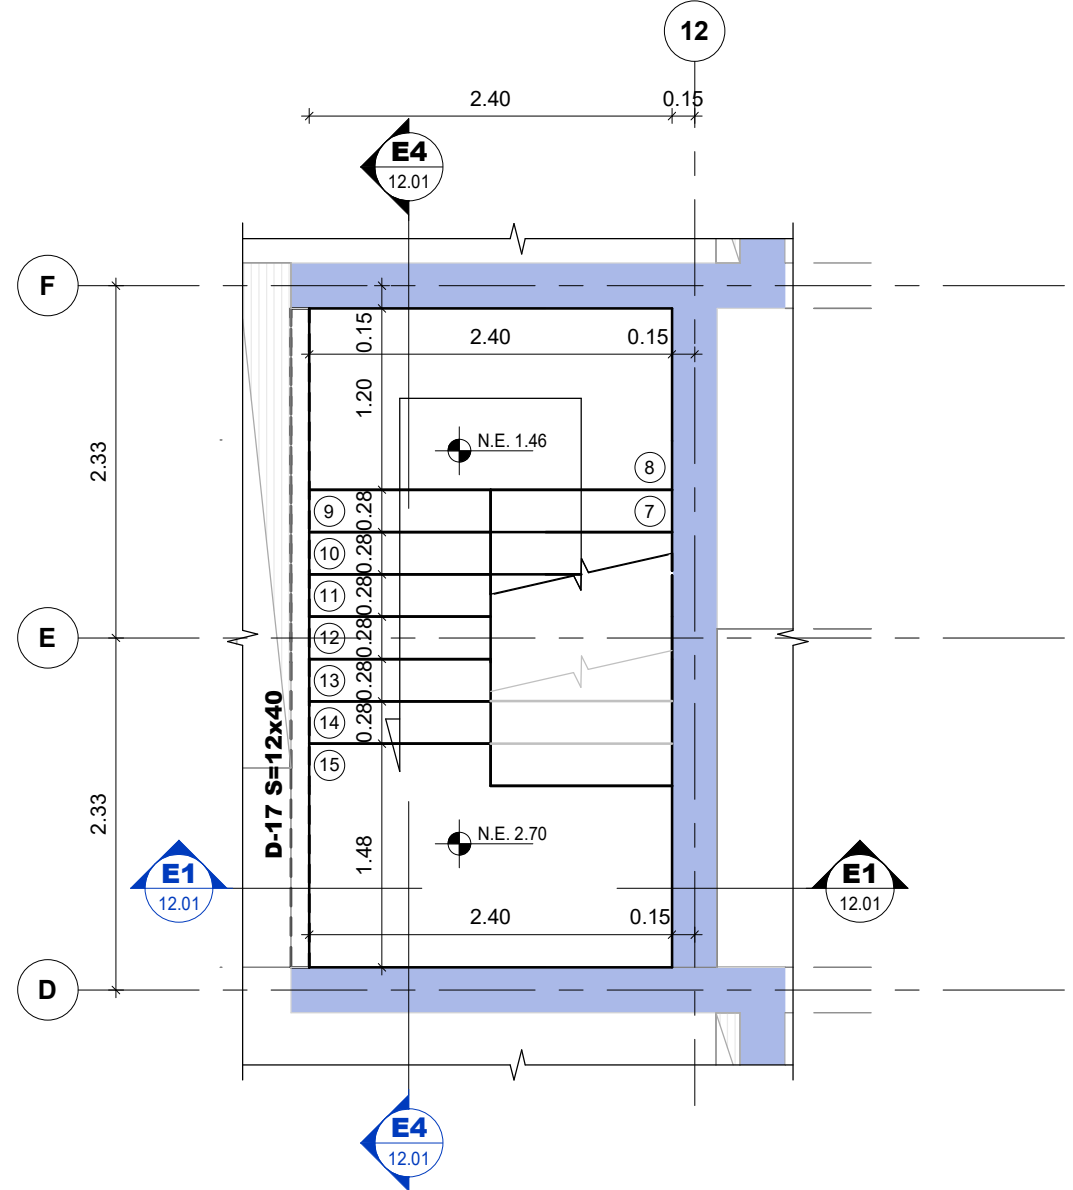


PLANTA LLEGADA ESCALERA TIPO 2 (PISO 1 A 2)
Escala 1 : 50

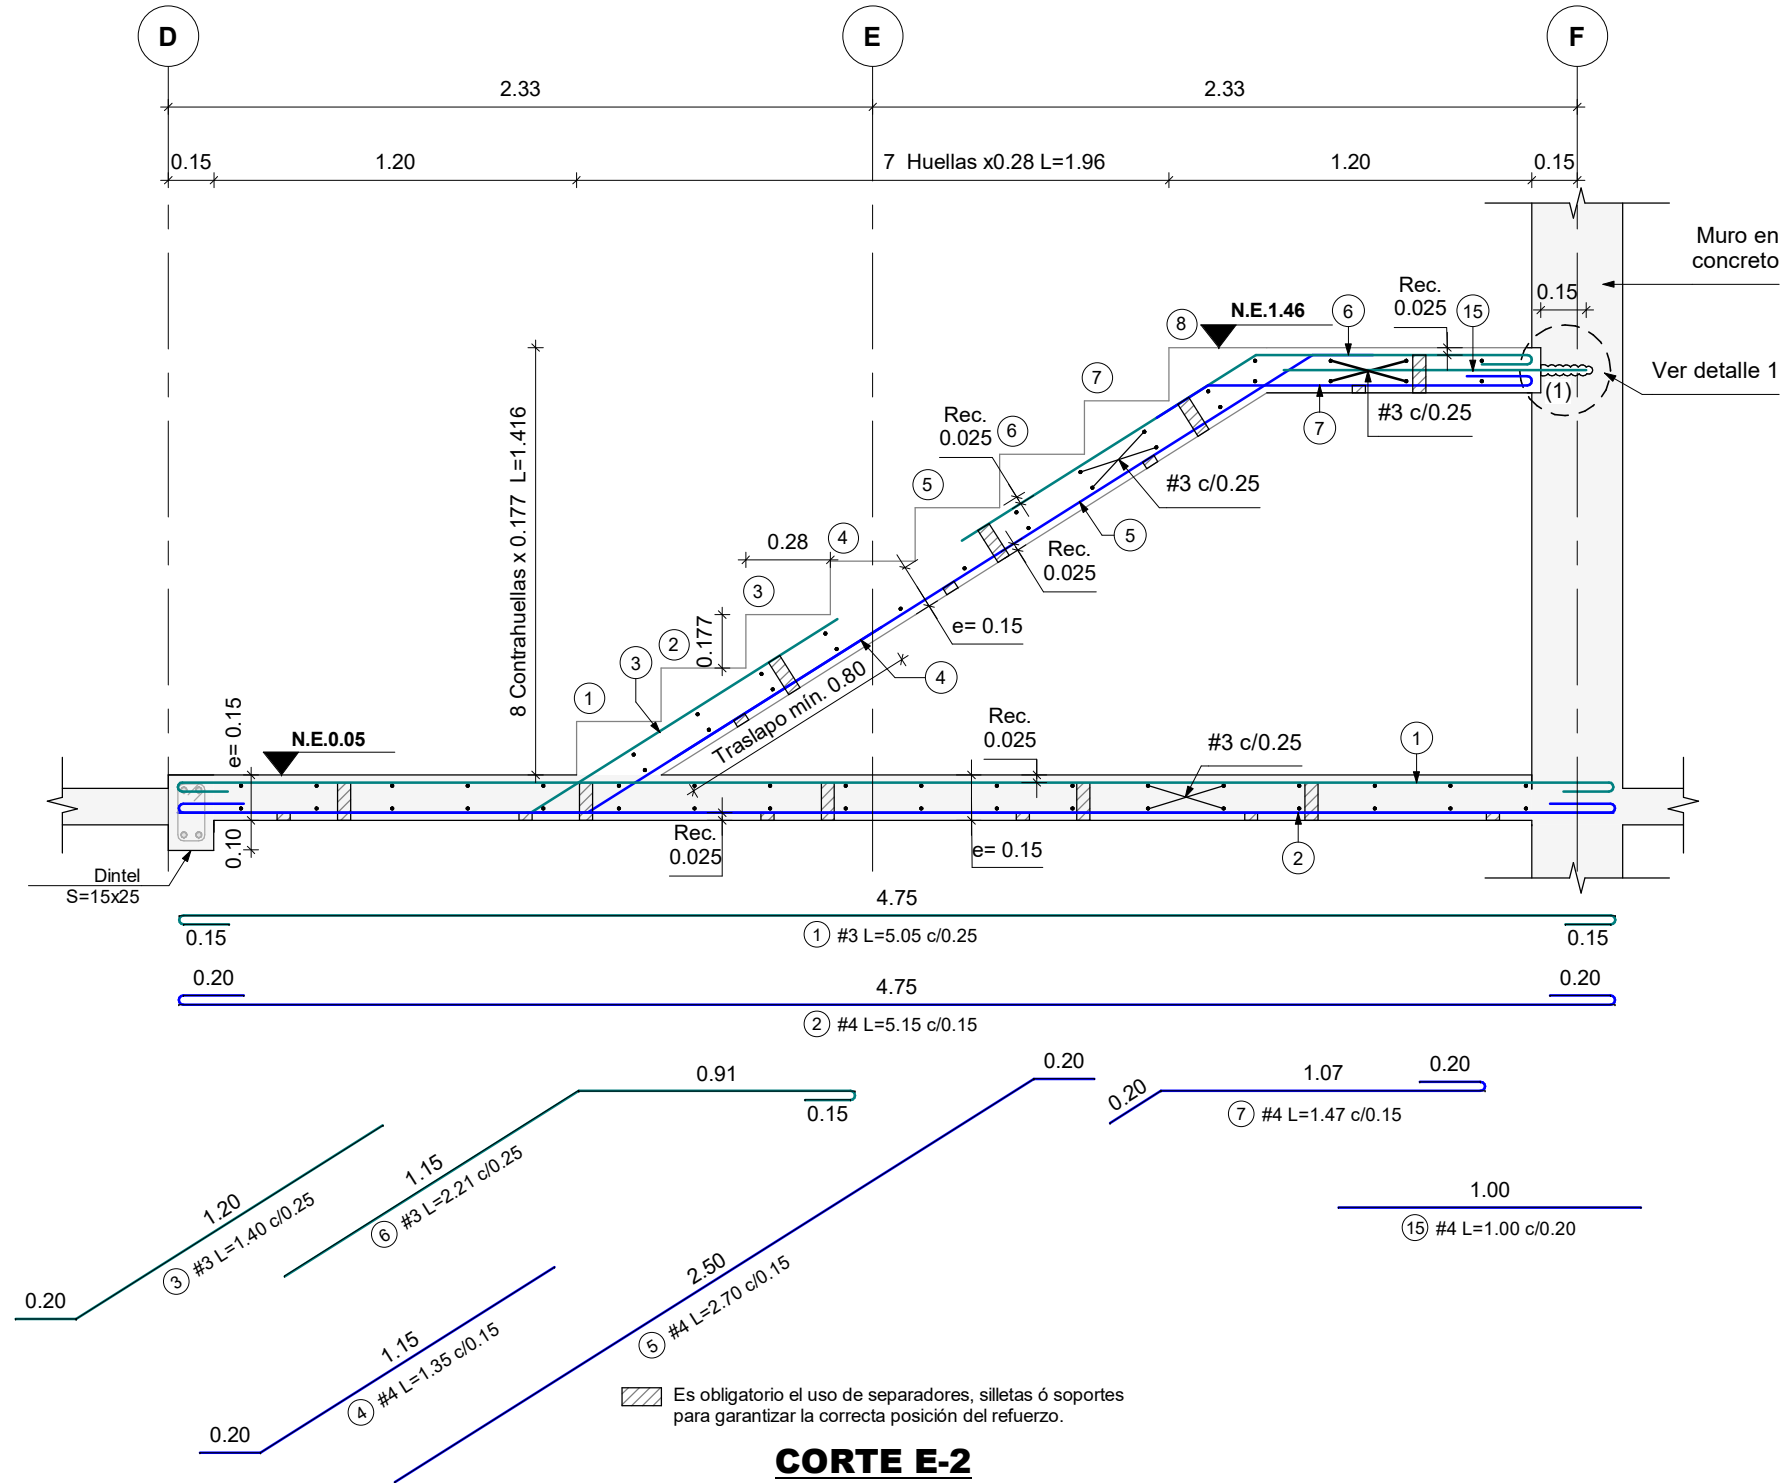


CORTE E-2
Escala 1 : 25

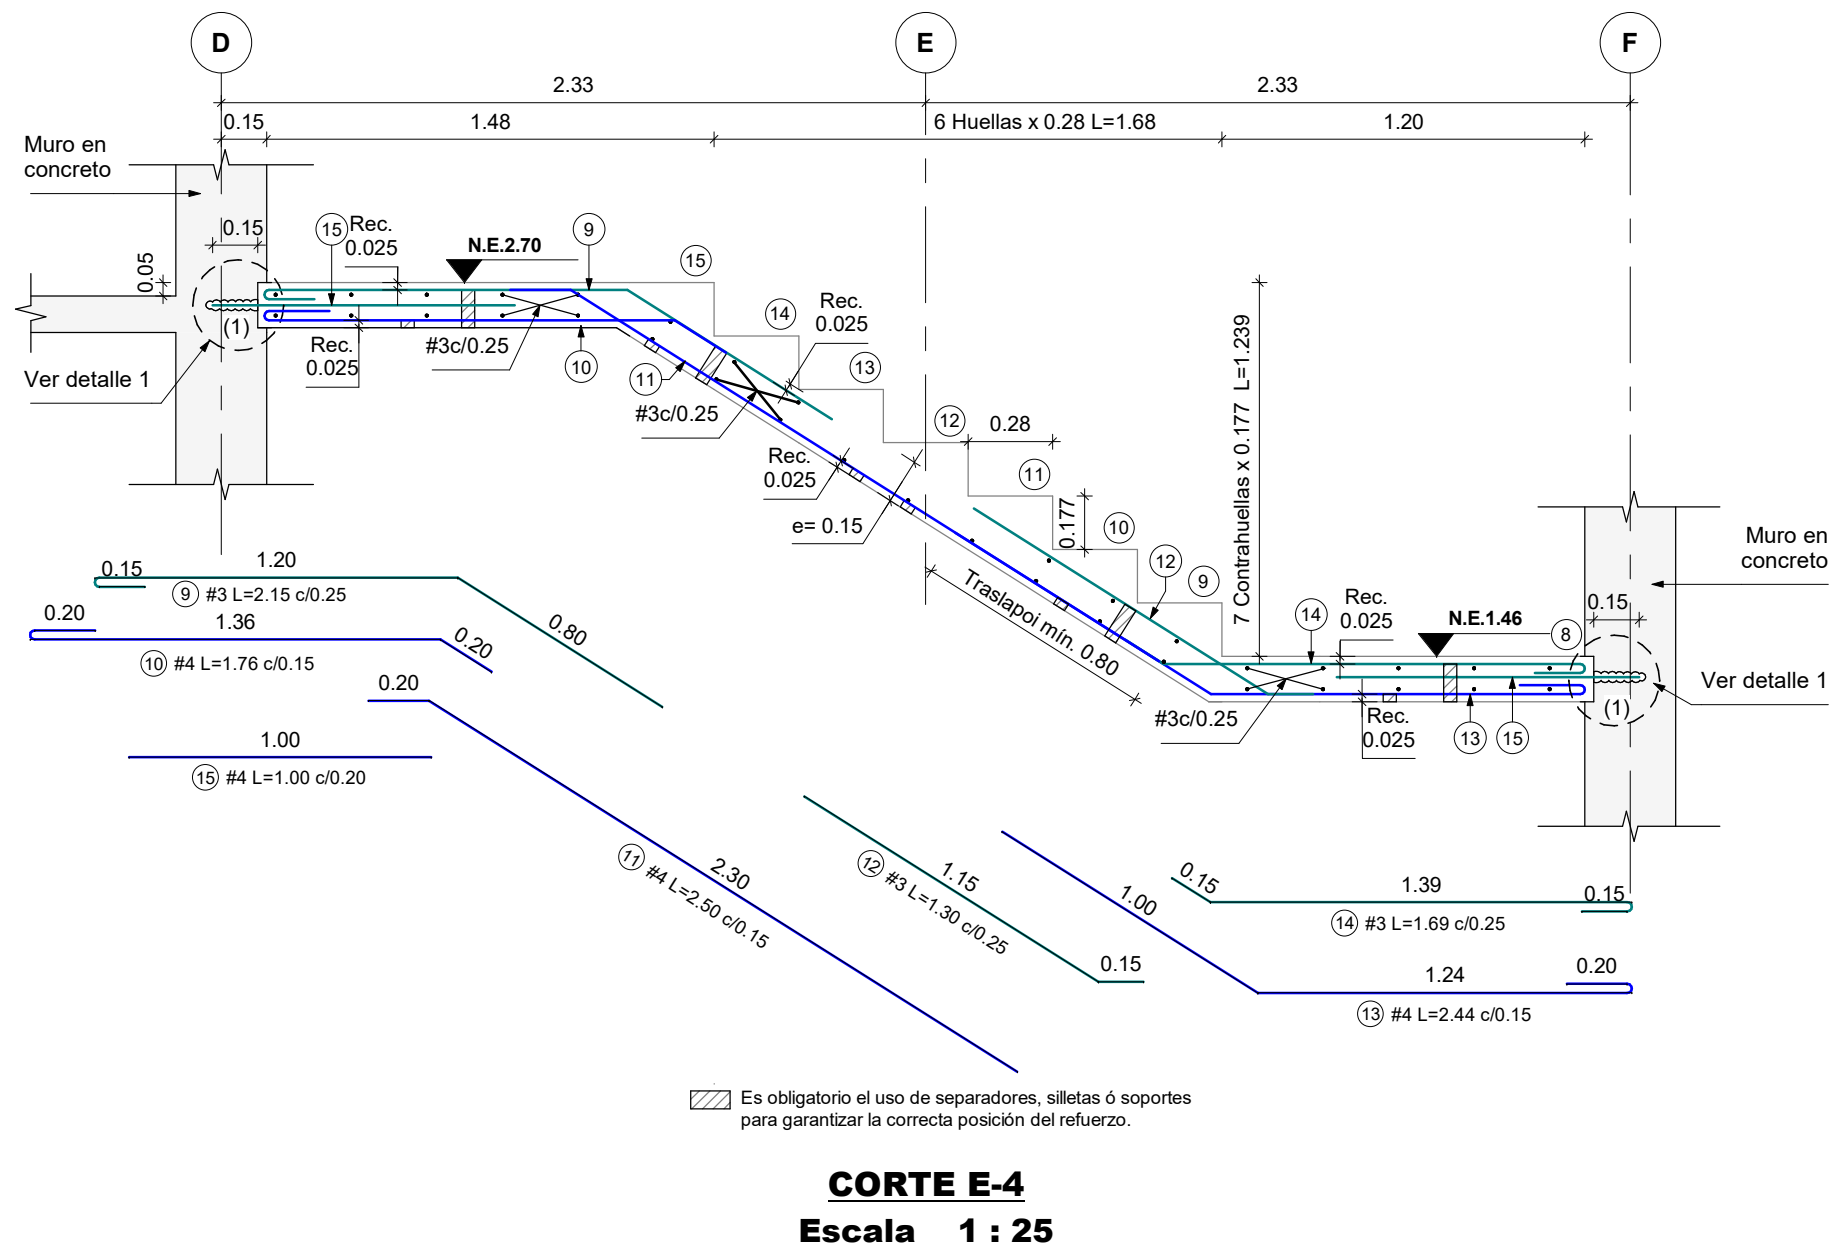

CORTE E-4
Escala 1 : 25

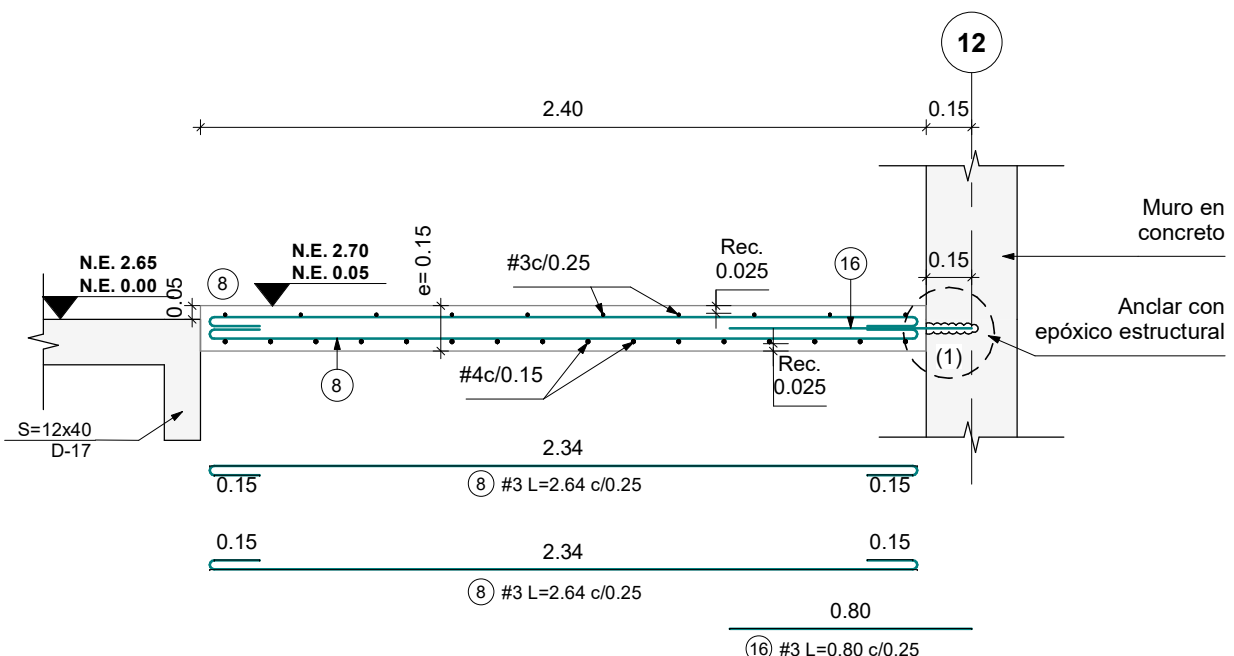

CORTE E-1
Escala 1 : 25

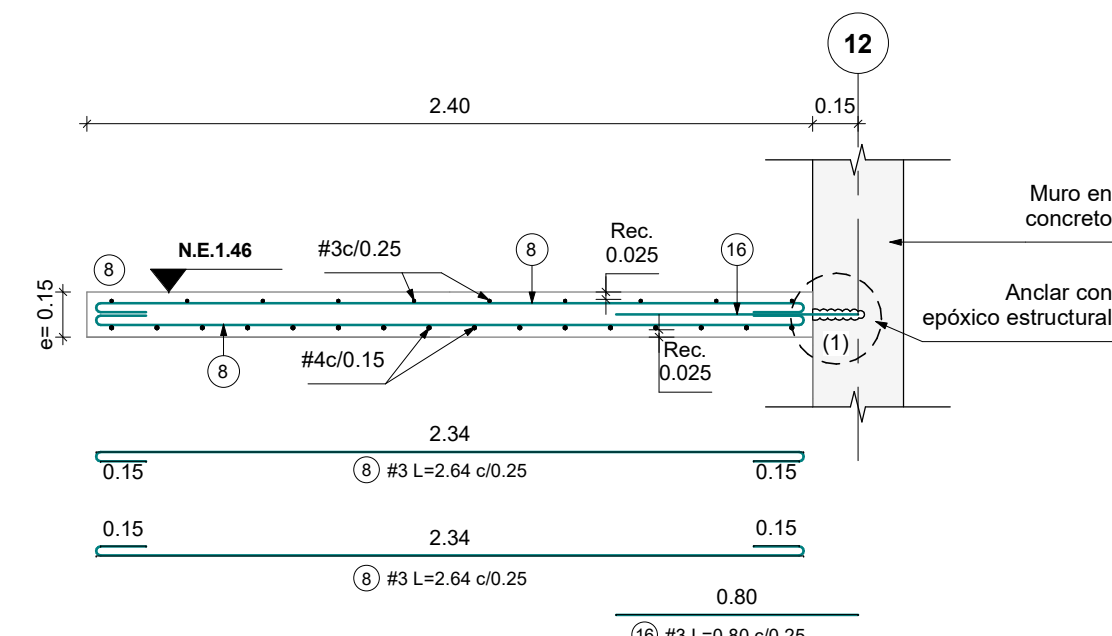

CORTE E-3
Escala 1 : 25

CONCRETO:
f'c=21 MPa
f'c=210 kg/cm²
f'c=3000 psi

NOTAS:
1. Ver detalles generales en PL N° 01.02

PLANO N° 12.01

VERSIÓN : 2

Aycardi Estructural

GERENTE DE PROYECTO
ROBERTO AYCARDI F.
MAT. 2520257258 CND

INGENIERO
CARLOS ANDRÉS WILCHES C.

MODELADOR
DANIEL CASTELLANOS

MODIFICACIONES	FECHA
Emisión Inicial	21-03-2025
Ajuste presentación	26-02-2026



LA SCALA

LA SCALA_EST_TOR-1

TORRE 1

CALLE 170 CON AV. BOYACA

DESPIECE ESCALERA TIPO 2 (PISO 1 A 2)

LA SCALA_EST_TOR-1_12.01_ESC-2

REVISOR ESTRUCTURAL
RAMÓN ANDRÉS ALVAREZ MANTILLA
MAT. 25202-346546 CND.

PLANO N° 12.01

VERSIÓN : 2