



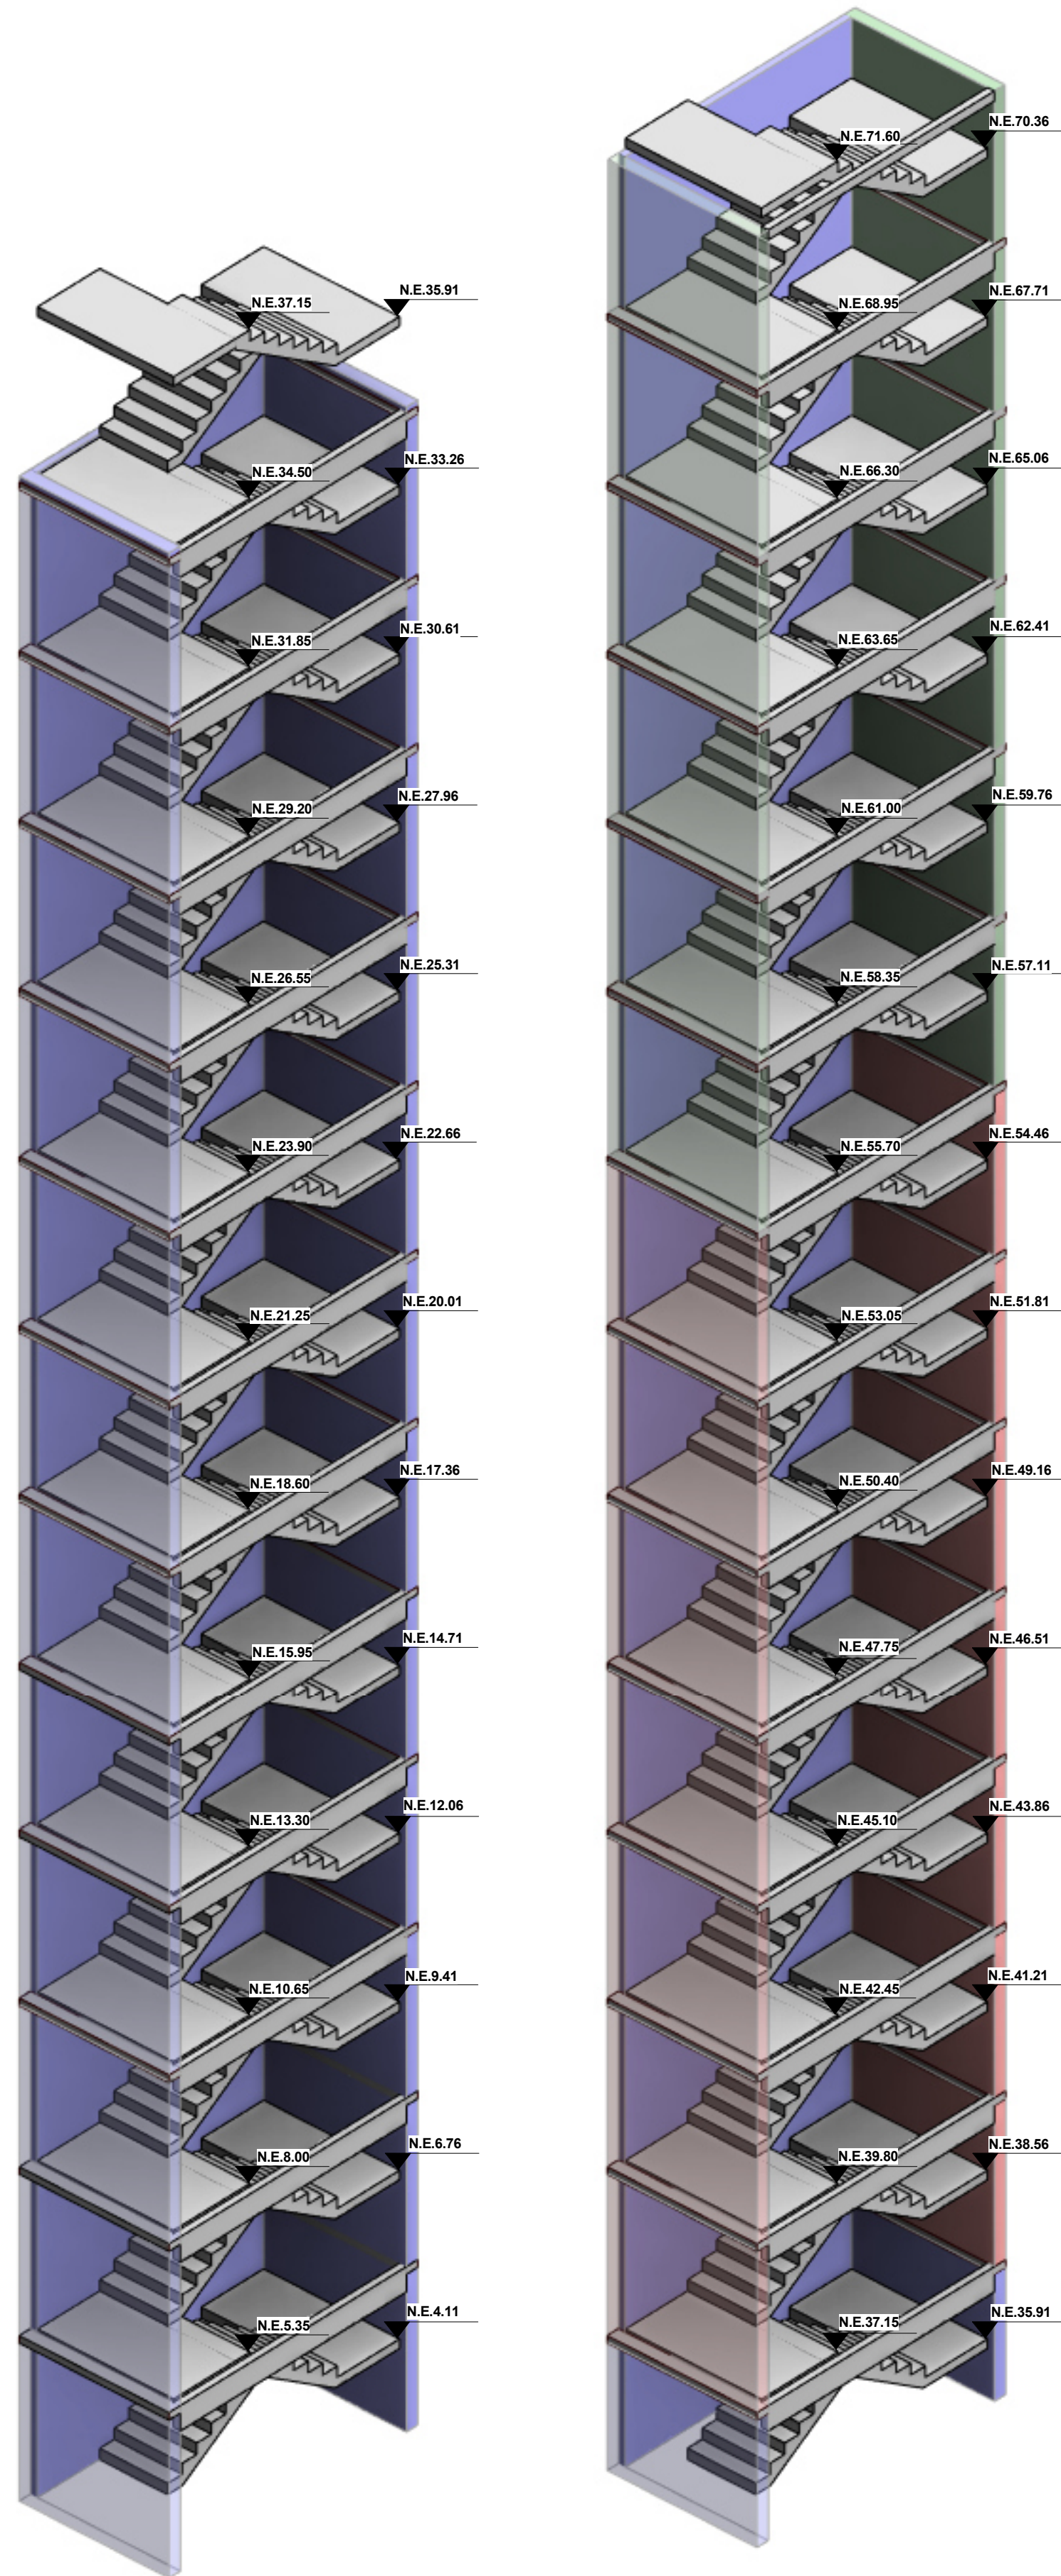


3D ESCALERAS TIPO 1 Y 2 DE PISO 2 A PISO 28
Sin escala


CUADRO NIVELES ESCALERA TIPO 2 DE PISO 2 A PISO 28					
ARRANQUE	LLEGADA	N1	N2	N3	
PISO 2	PISO 3	2.70	4.11	5.35	
PISO 3	PISO 4	5.35	6.76	8.00	
PISO 4	PISO 5	8.00	9.41	10.65	
PISO 5	PISO 6	10.65	12.06	13.30	
PISO 6	PISO 7	13.30	14.71	15.95	
PISO 7	PISO 8	15.95	17.36	18.60	
PISO 8	PISO 9	18.60	20.01	21.25	
PISO 9	PISO 10	21.25	22.66	23.90	
PISO 10	PISO 11	23.90	25.31	26.55	
PISO 11	PISO 12	26.55	27.96	29.20	
PISO 12	PISO 13	29.20	30.61	31.85	
PISO 13	PISO 14	31.85	33.26	34.50	
PISO 14	PISO 15	34.50	35.91	37.15	
PISO 15	PISO 16	37.15	38.56	39.80	
PISO 16	PISO 17	39.80	41.21	42.45	
PISO 17	PISO 18	42.45	43.86	45.10	
PISO 18	PISO 19	45.10	46.51	47.75	
PISO 19	PISO 20	47.75	49.16	50.40	
PISO 20	PISO 21	50.40	51.81	53.05	
PISO 21	PISO 22	53.05	54.46	55.70	
PISO 22	PISO 23	55.70	57.11	58.35	
PISO 23	PISO 24	58.35	59.76	61.00	
PISO 24	PISO 25	61.00	62.41	63.55	
PISO 25	PISO 26	63.55	65.06	66.30	
PISO 26	PISO 27	66.30	67.71	69.35	
PISO 27	PISO 28	68.95	70.36	71.60	

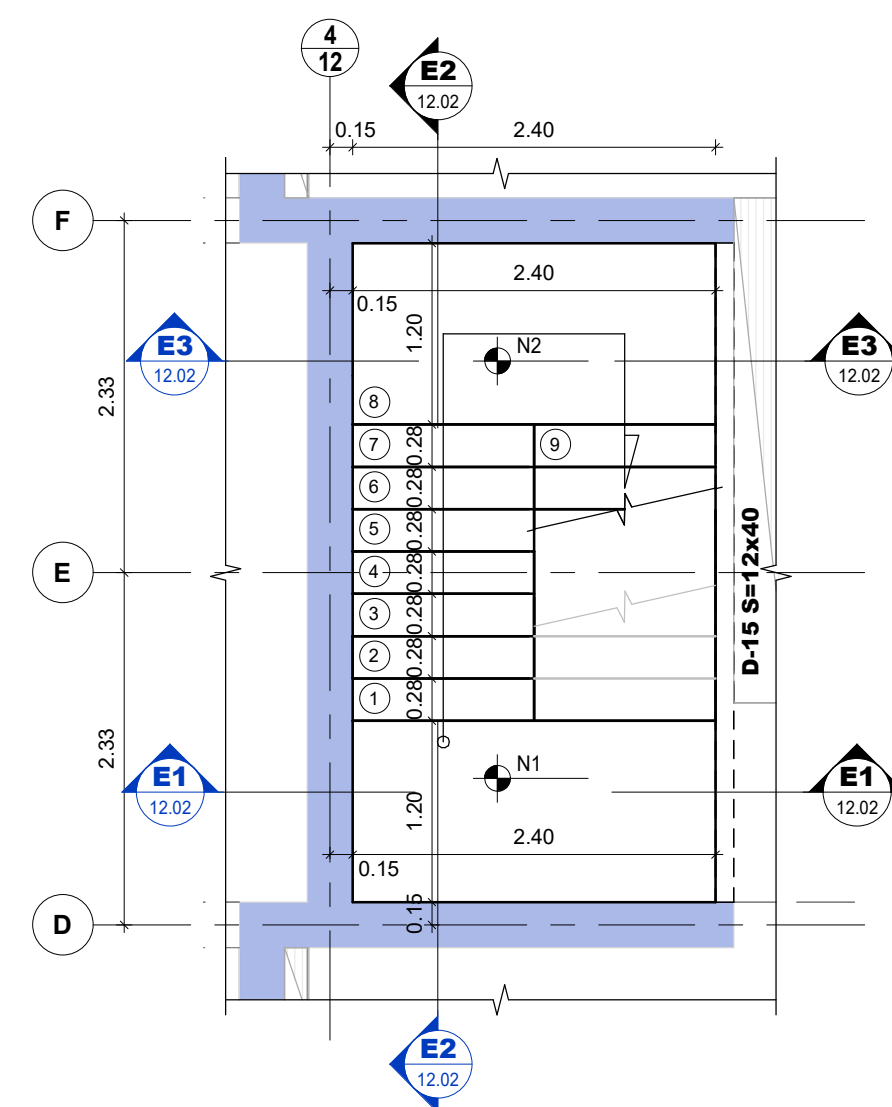


PLANTA ARRANQUE ESCALERAS TIPO 1 Y 2 (PISO 3 A 28)
Escala 1 : 50

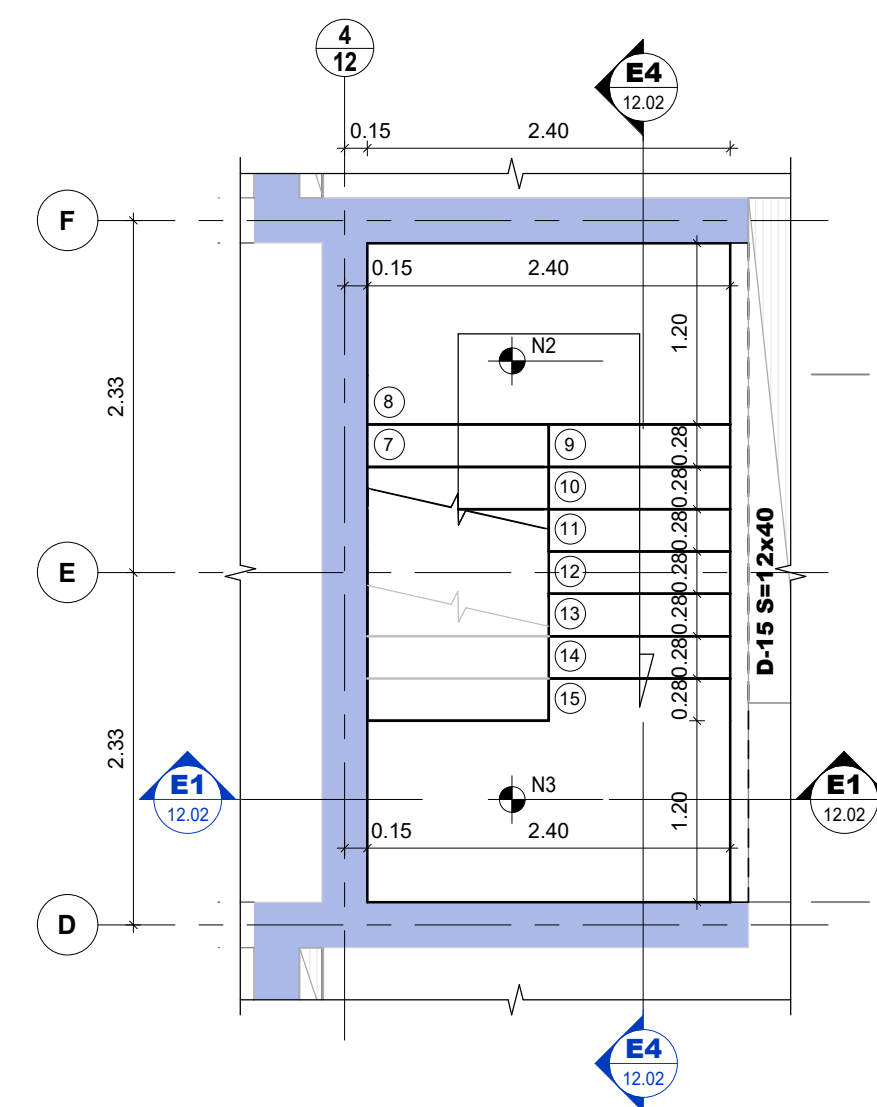


PLANTA LLEGADA ESCALERAS TIPO 1 Y 2 (PISO 3 A 28)
Escala 1 : 50

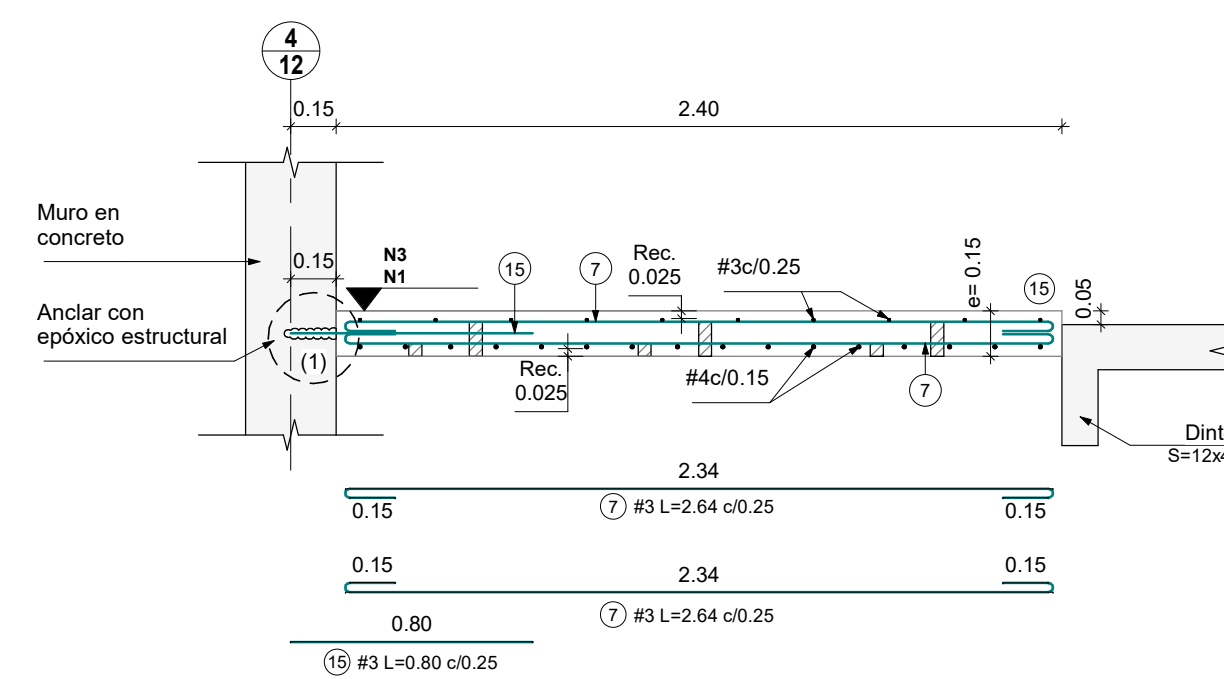


CORTE E-1
Escala 1 : 25

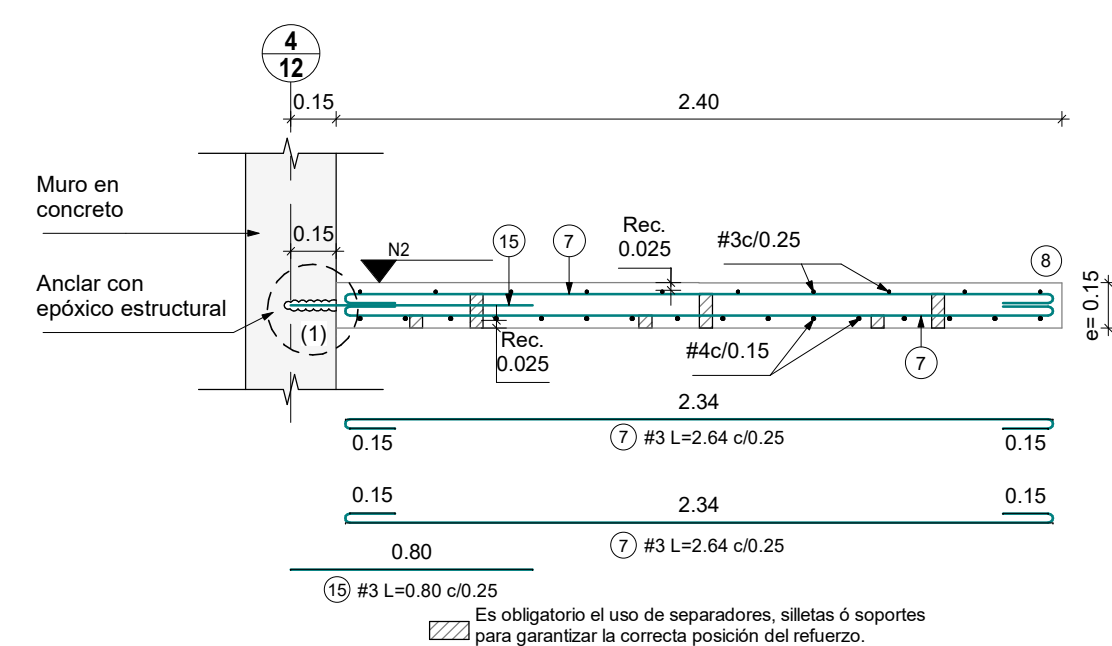


CORTE E-2
Escala 1 : 25

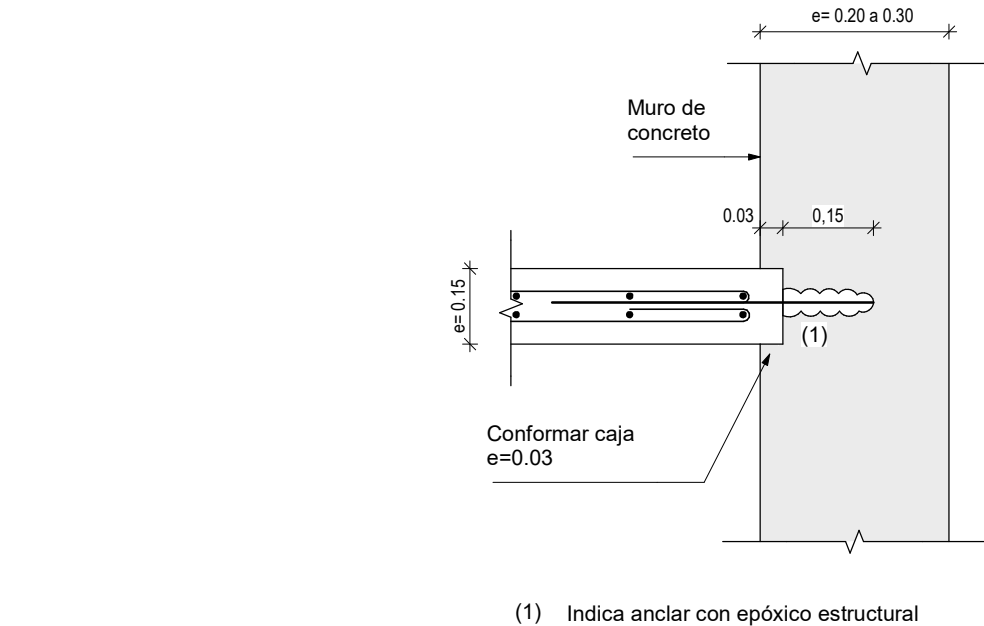


CORTE E-3
Escala 1 : 25

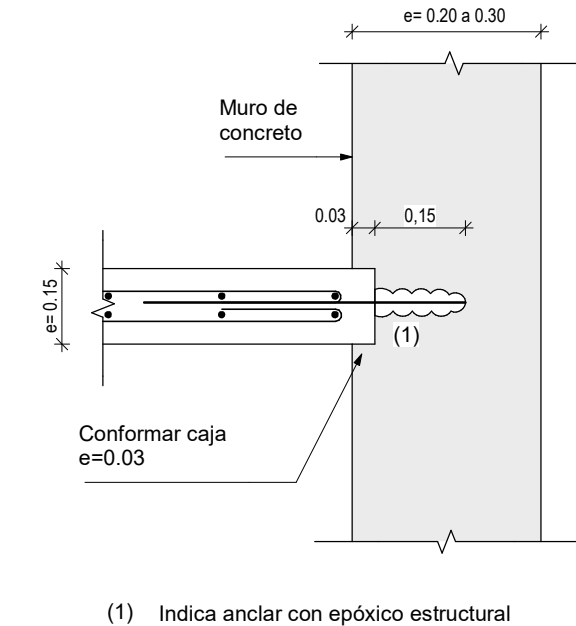

DETALLE 1
Escala 1 : 10

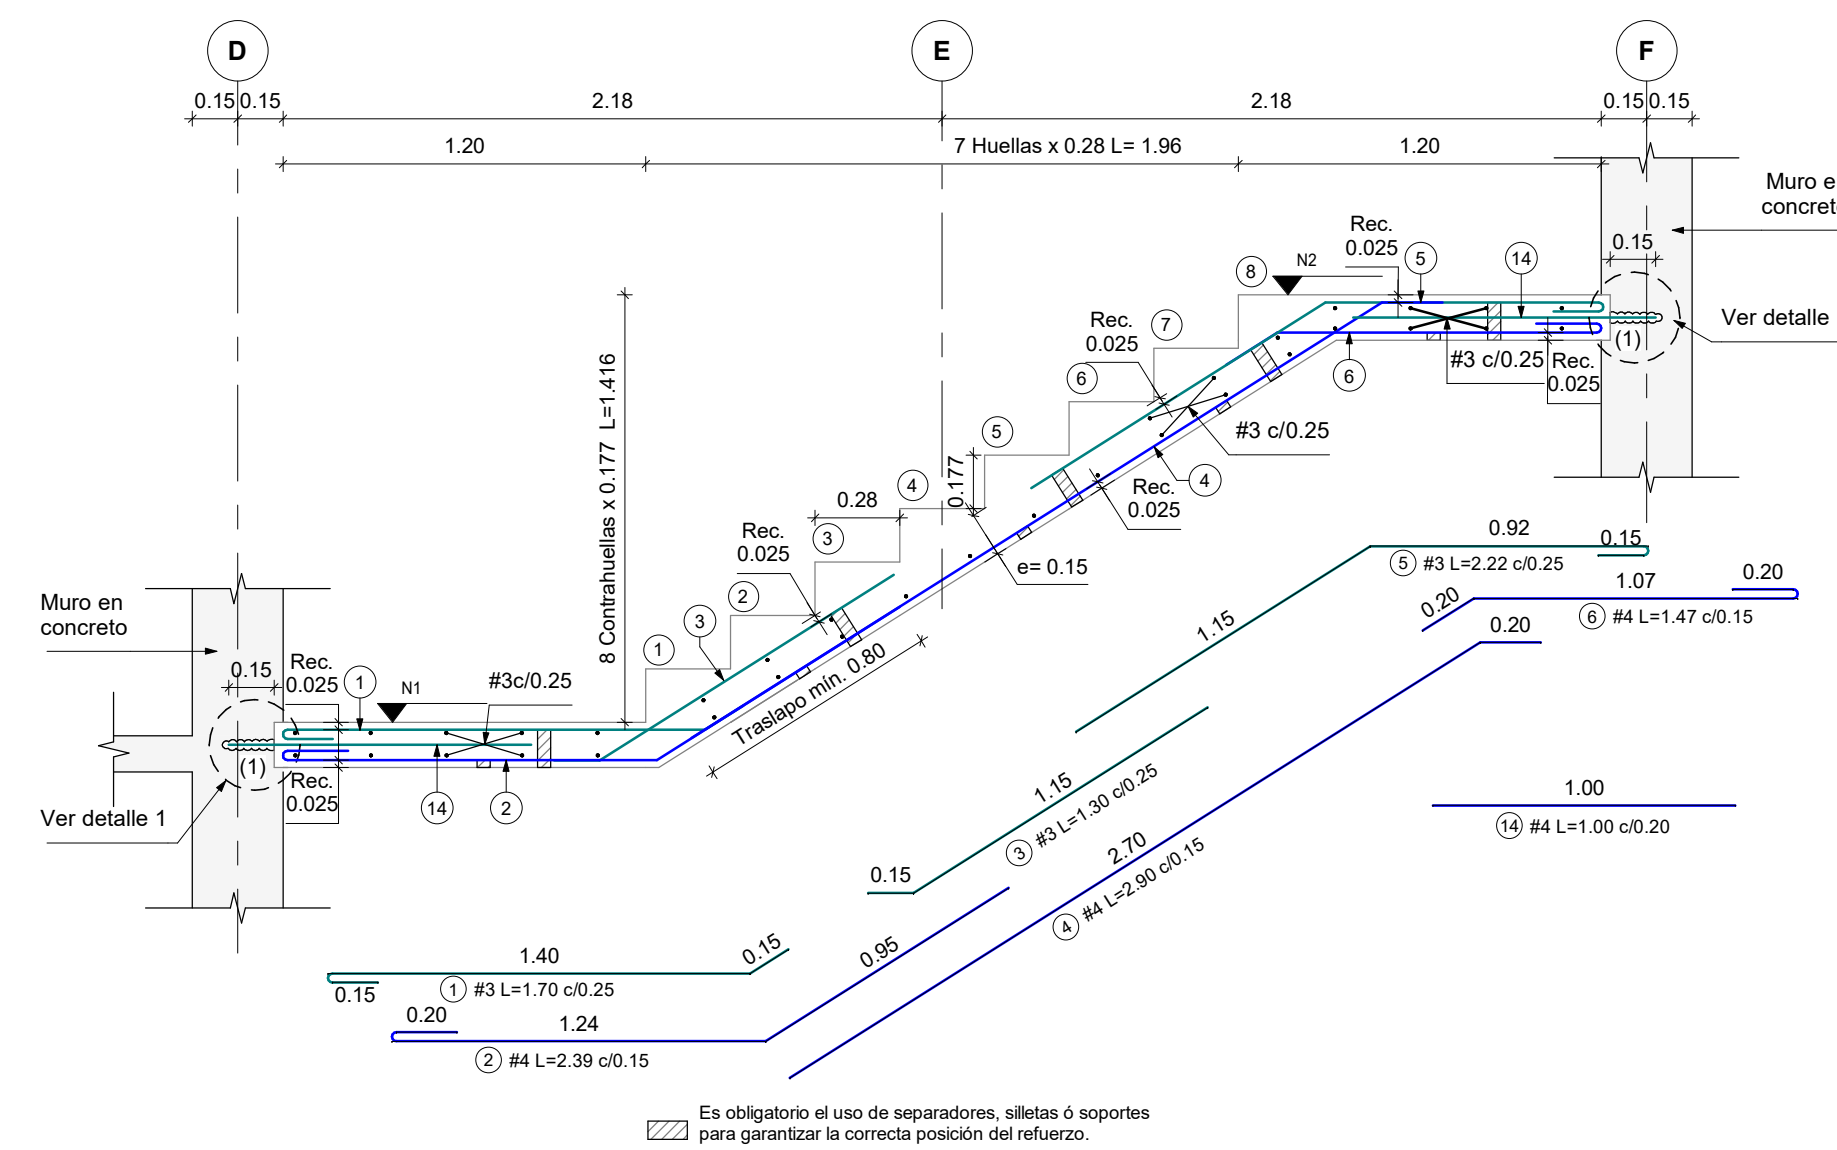

CORTE E-5
Escala 1 : 25

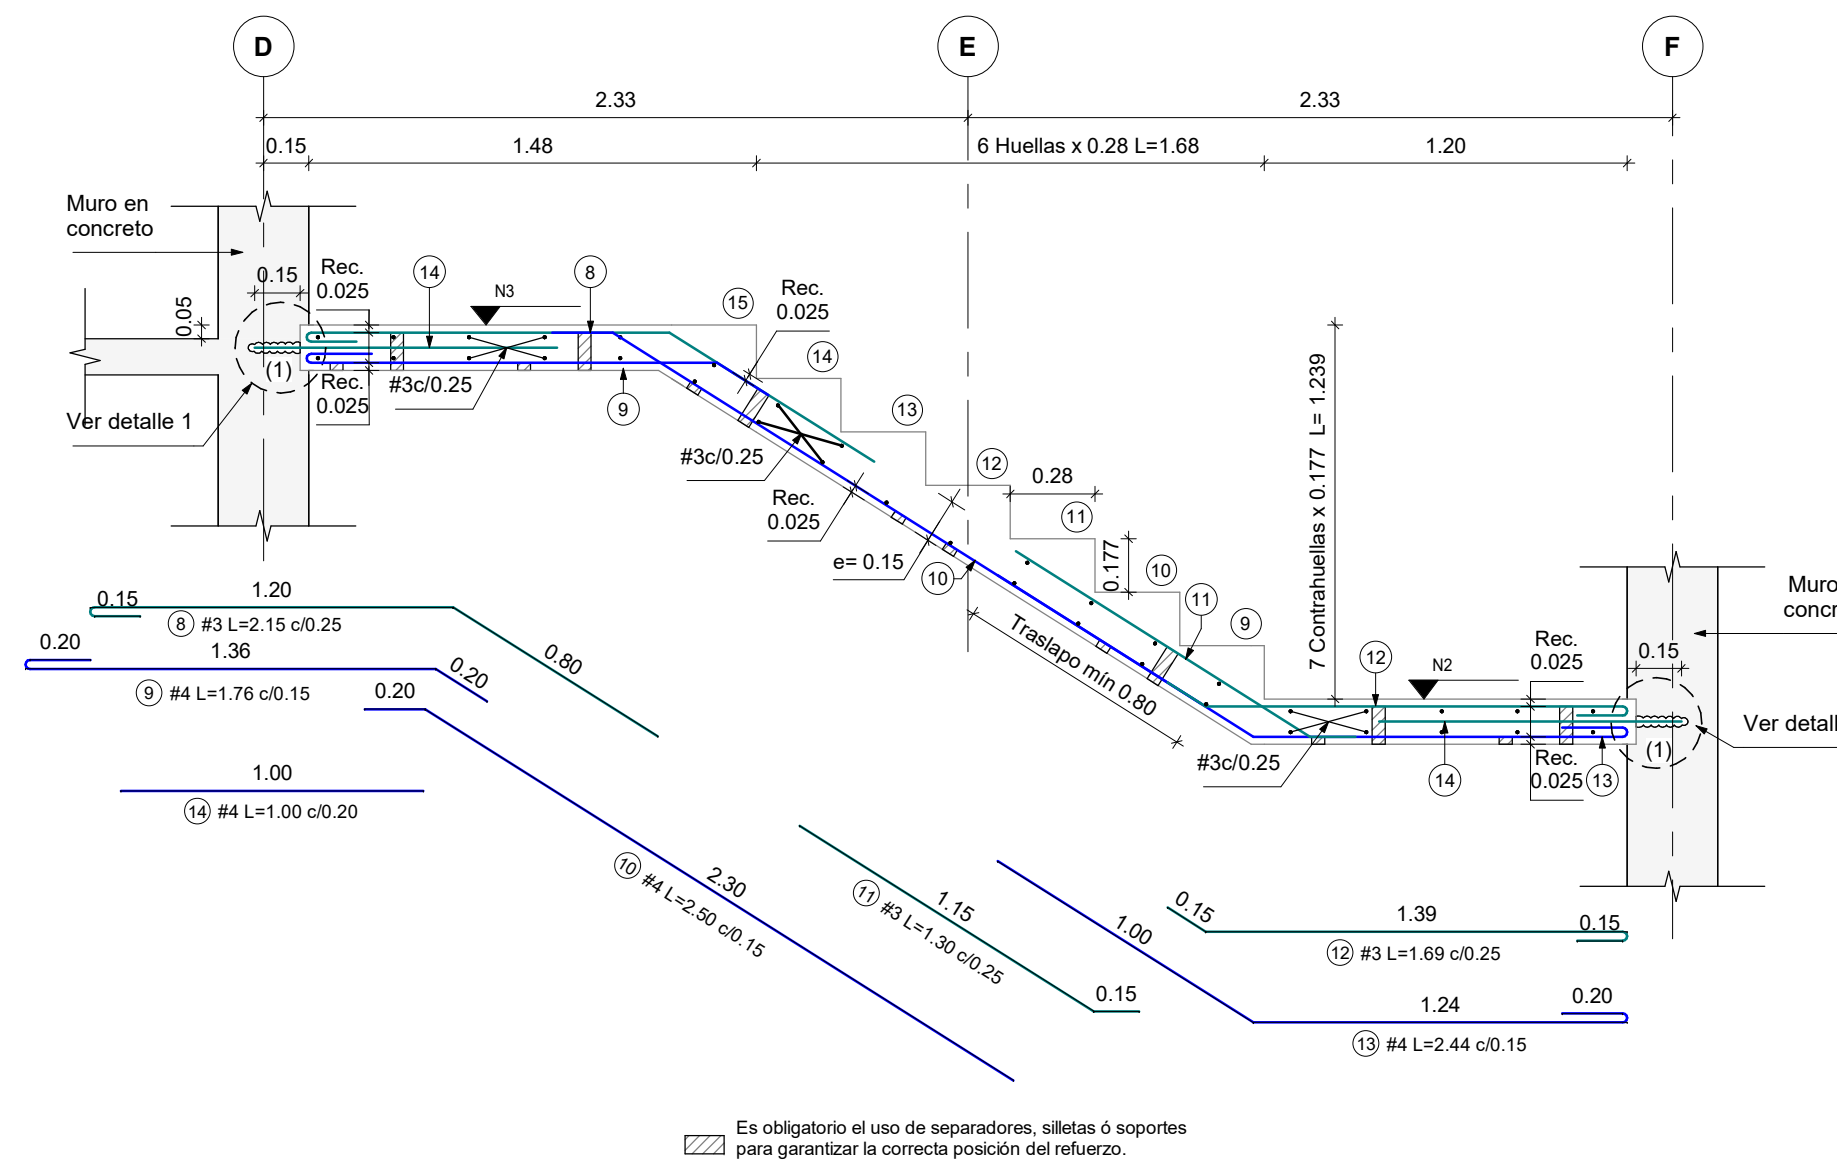

CORTE E-6
Escala 1 : 25

MODIFICACIONES	FECHA
Emisión Inicial	21-03-2025
Ajuste presentación	26-02-2026



LA SCALA

LA SCALA_EST_TOR-1

TORRE 1

CALLE 170 CON AV. BOYACA

DESPIECE ESCALERAS TIPO 1 Y 2 (PISO 3 A 28)

LA SCALA_EST_TOR-1_12.02_ESC-1

REVISOR ESTRUCTURAL

RAMÓN ANDRÉS ALVAREZ MANTILLA
MAT. 25202-346546 CND.

CONCRETO:
f_c=21 MPa
f_c=210 kg/cm²
f_c=3000 psi

NOTAS:
1. Ver detalles generales en PL N° 01.02