




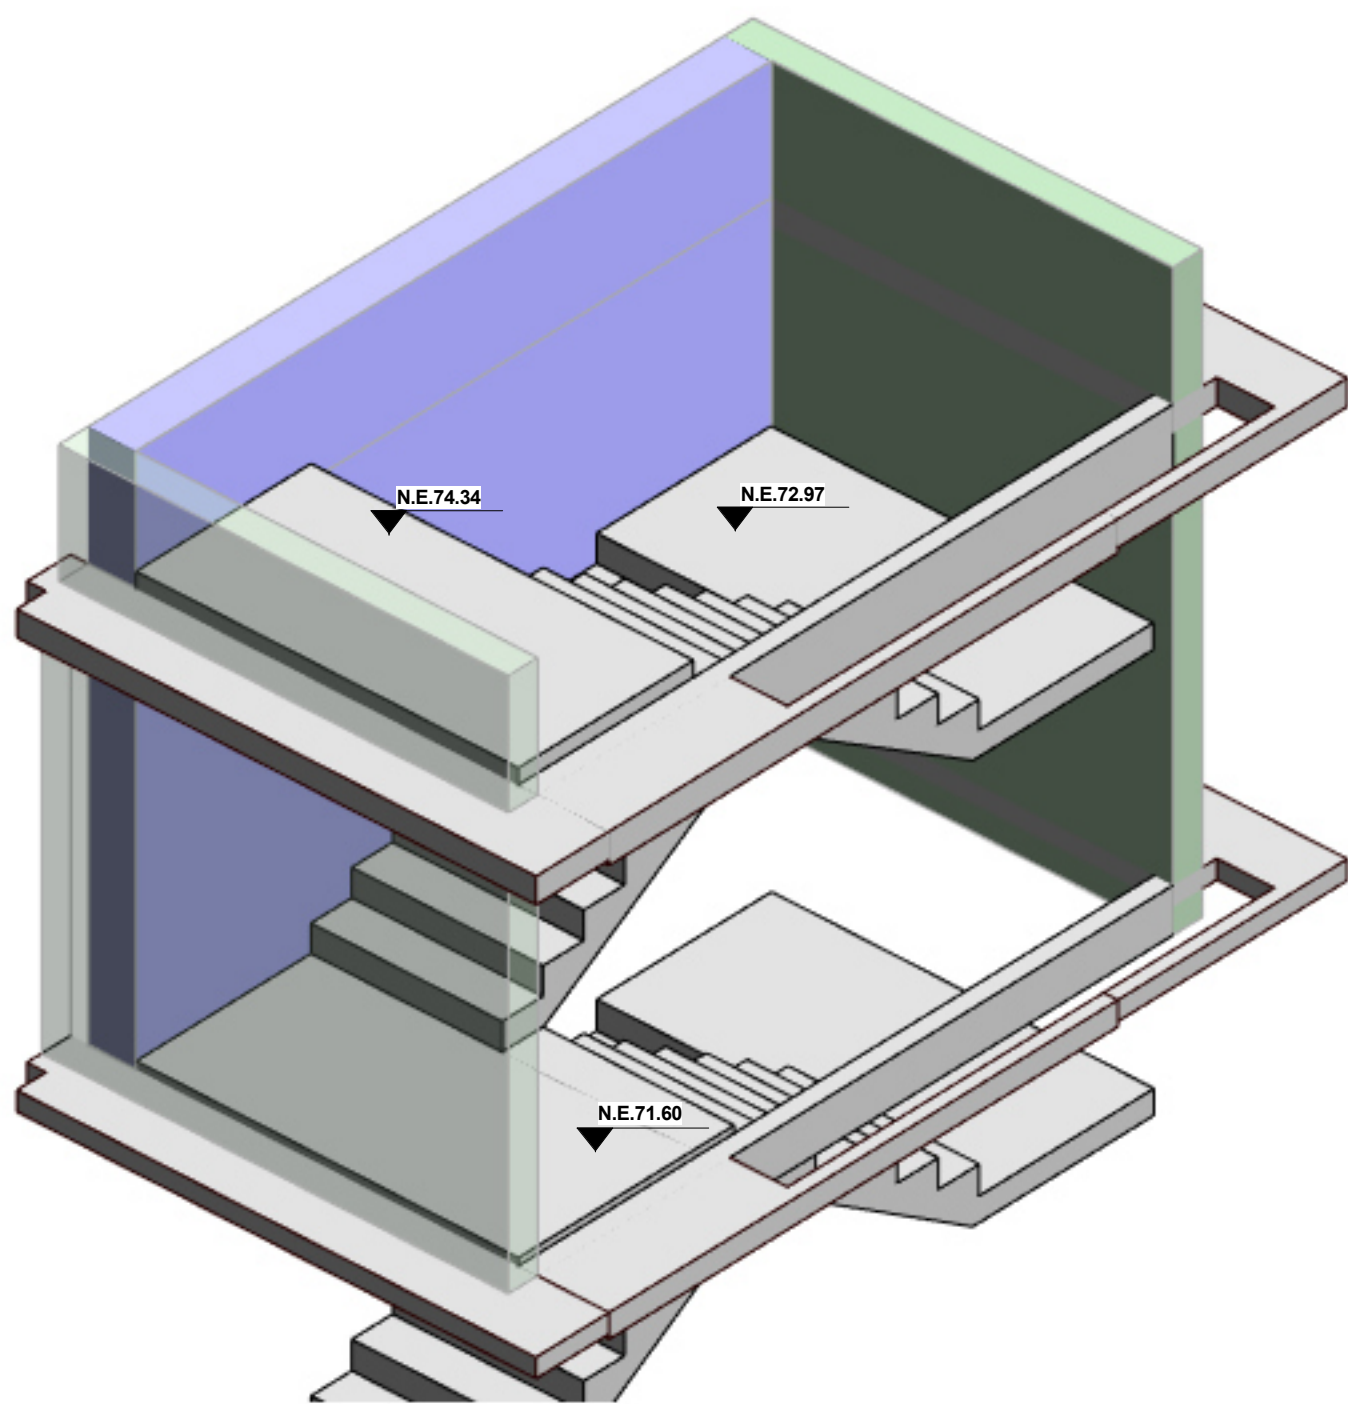


3D ESCALERAS TIPO 1 Y 2 (PISO 28 A CUBIERTA)
Sin escala

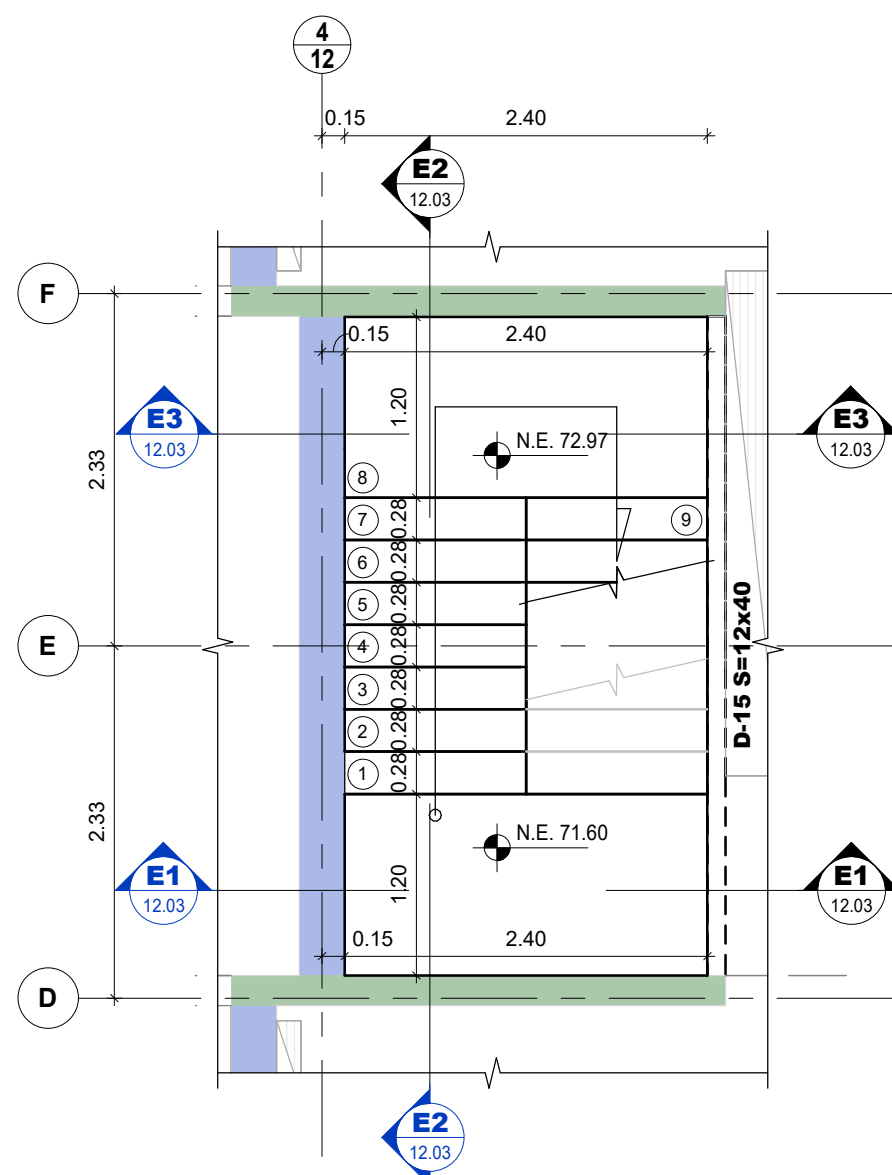


PLANTA ARRANQUE ESCALERA TIPO 1 Y 2 (PISO 28 A CUBIERTA)
Escala 1:50

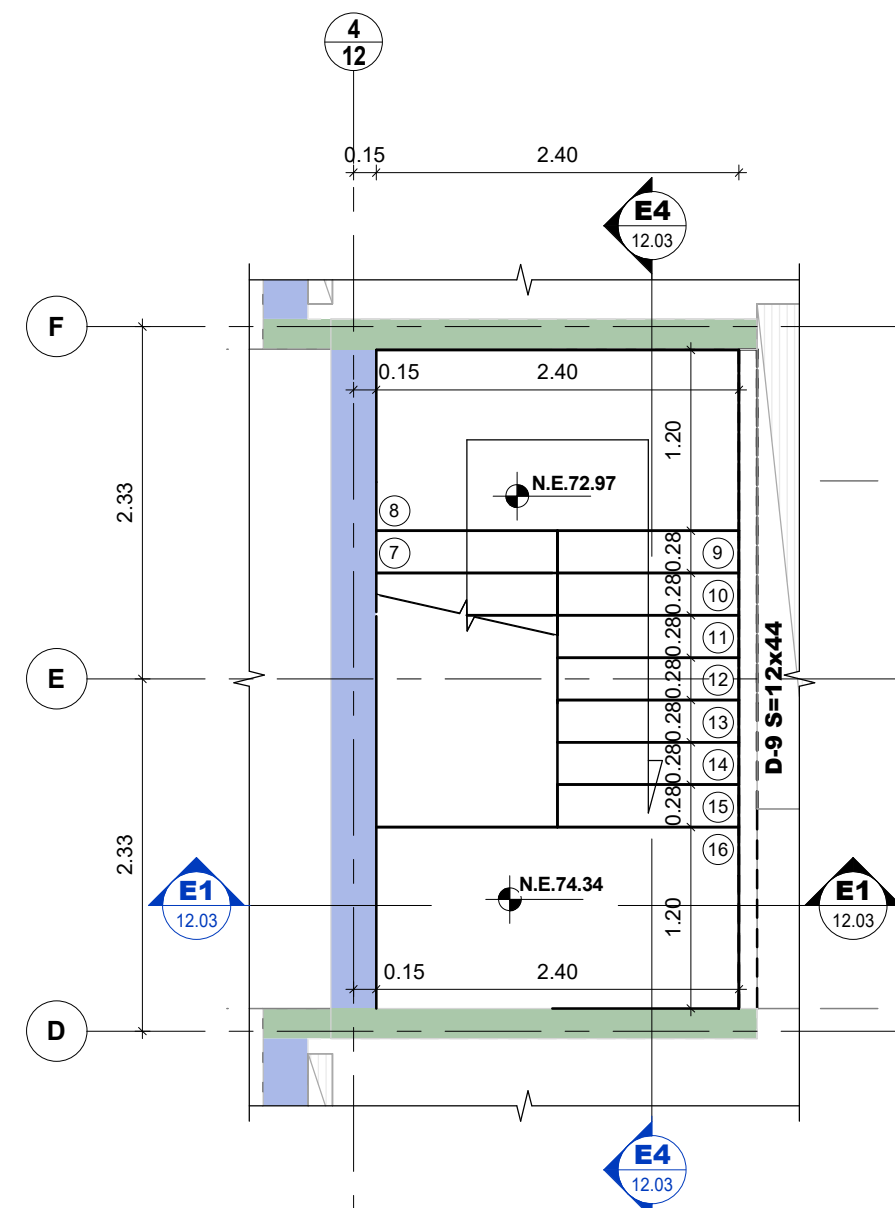


PLANTA LLEGADA ESCALERA TIPO 1 Y 2 (PISO 28 A CUBIERTA)
Escala 1:50

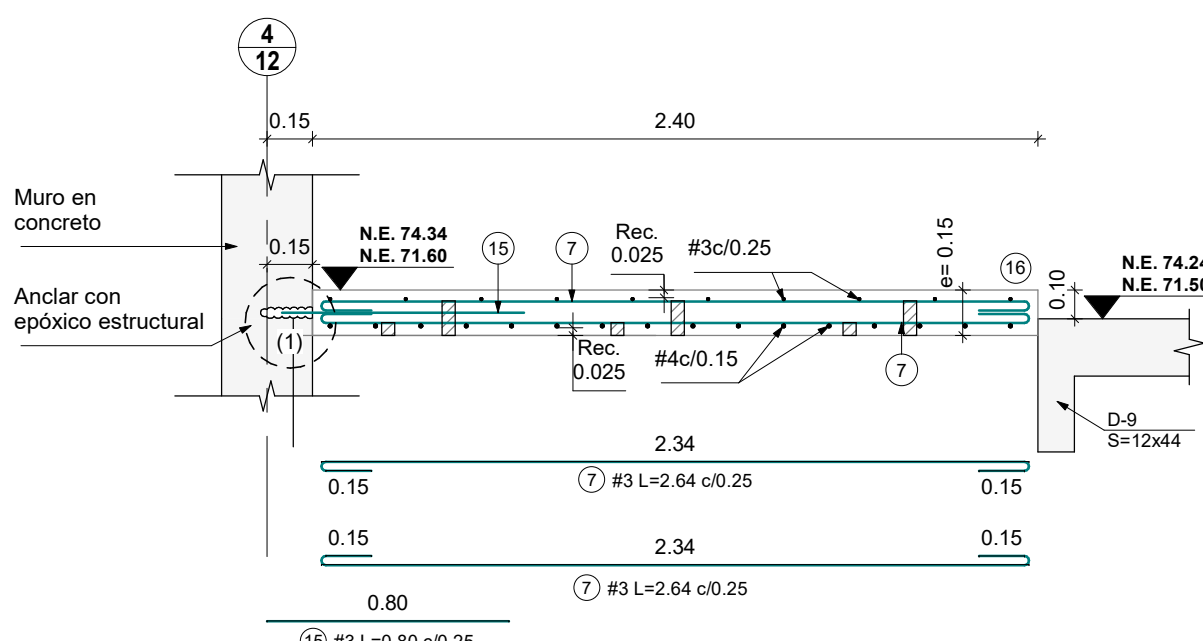


CORTE E-1
Escala 1:25

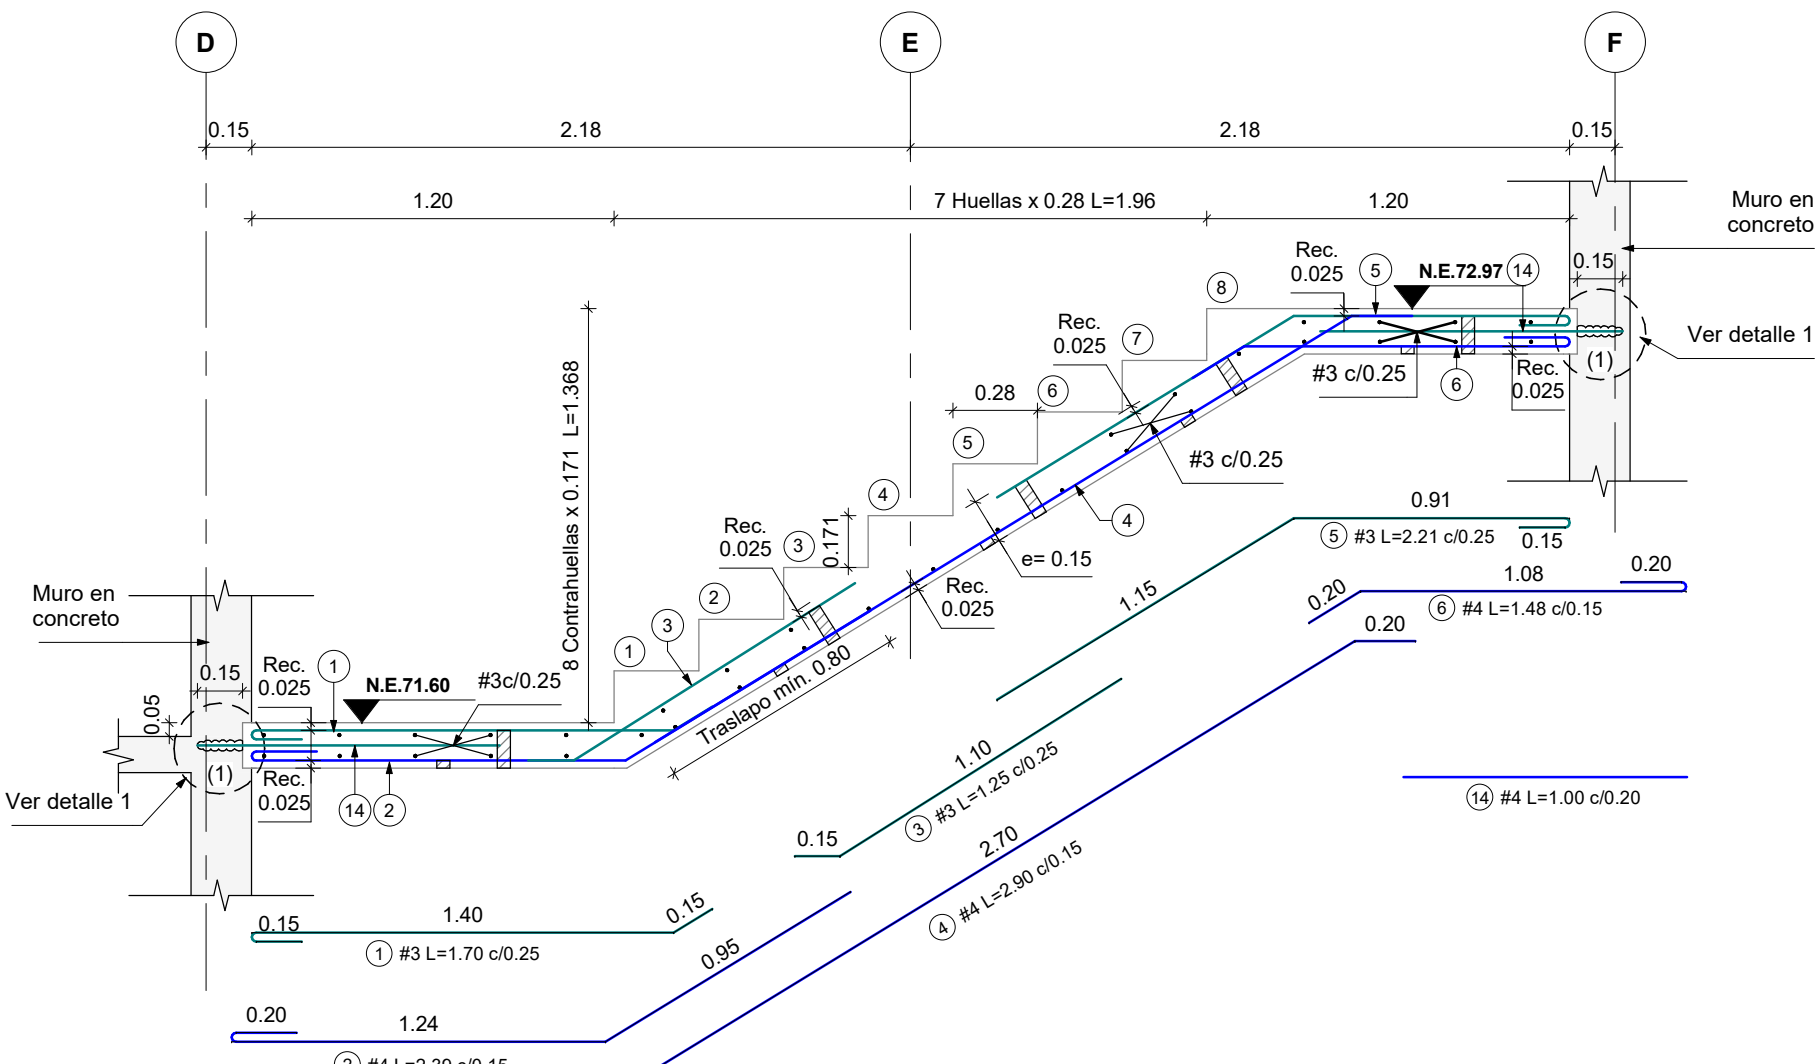


CORTE E-2
Escala 1:25

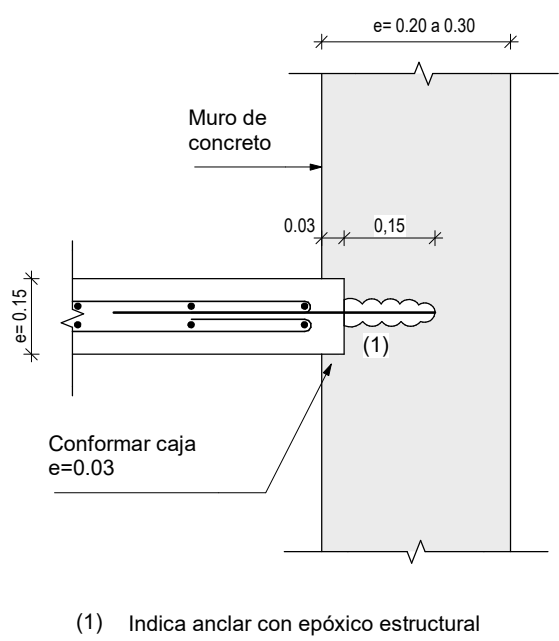

DETALLE 1
Escala 1:10

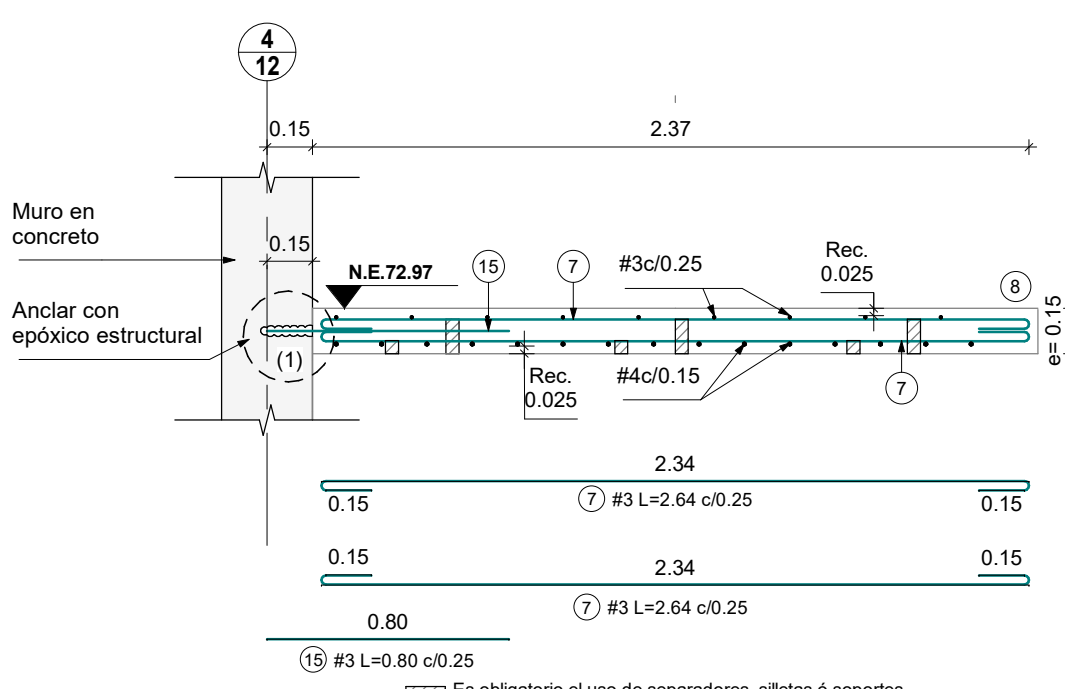

CORTE E-3
Escala 1:25

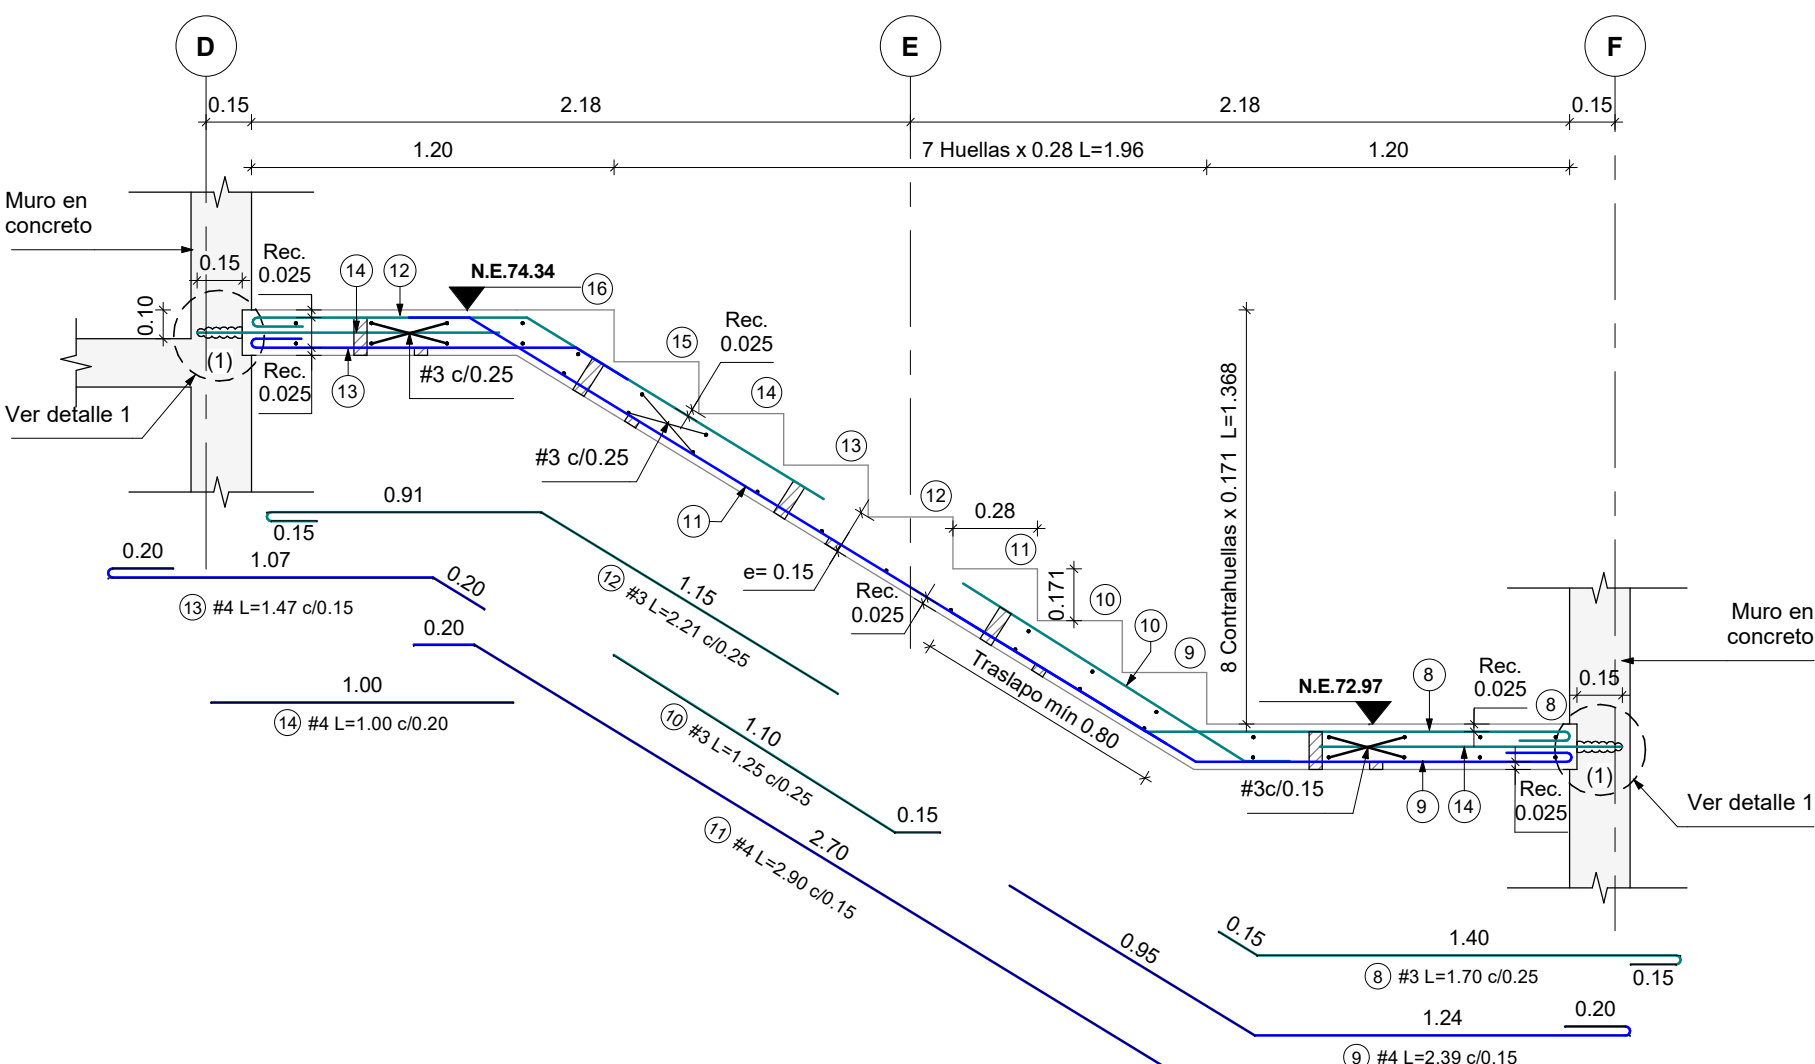

CORTE E-4
Escala 1:25

CONCRETO:
f_c=21 MPa
f_c=210 kg/cm²
f_c=3000 psi

NOTAS:
1. Ver detalles generales en PL N° 01.02

PLANO N° 12.03

VERSIÓN: 2



GERENTE DE PROYECTO
ROBERTO AYCARDI F.
MAT. 2520257258 CND

INGENIERO
CARLOS ANDRÉS WILCHES C.

MODELADOR
DANIEL CASTELLANOS

MODIFICACIONES	FECHA
Emisión Inicial	21-03-2025
Ajuste presentación	26-02-2026



LA SCALA

LA SCALA_EST_TOR-1

TORRE 1

CALLE 170 CON AV. BOYACA

DESPIECE ESCALERA TIPO 1 Y 2 (PISO 28 A CUBIERTA)

LA SCALA_EST_TOR-1_12.03_ESC-1

REVISOR ESTRUCTURAL
RAMÓN ANDRÉS ALVAREZ MANTILLA
MAT. 25202-346546 CND.

PLANO N°

VERSIÓN:

12.03

2

