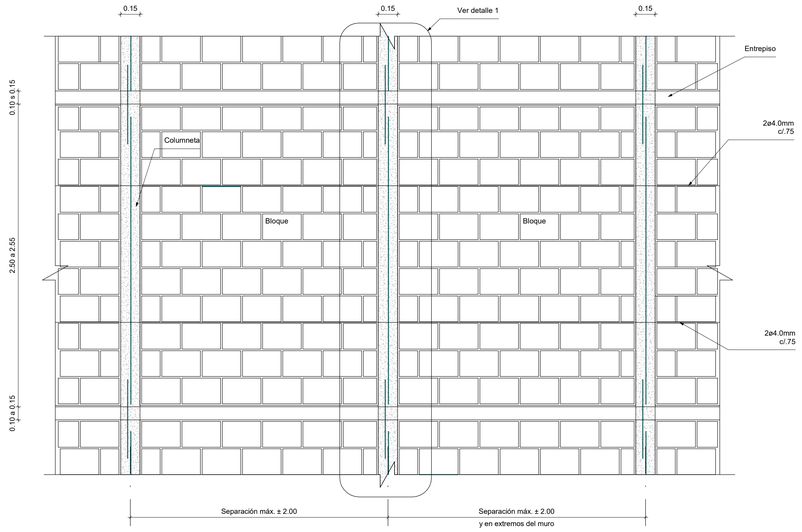

ELEVACIÓN DE MURO DIVISORIO
Escala 1 : 20

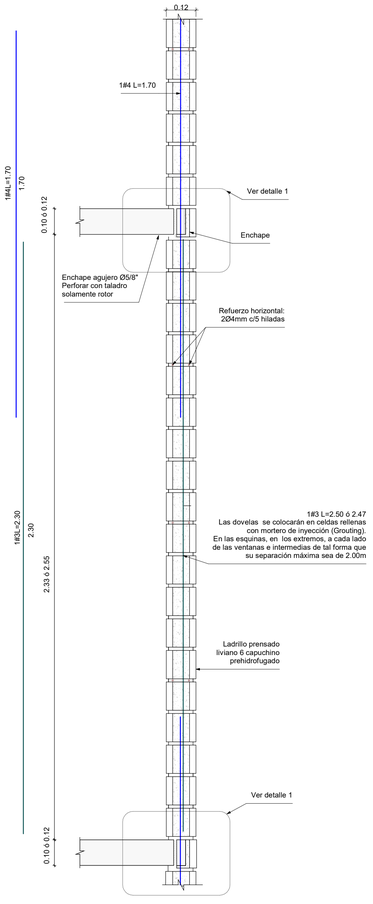

MUROS EN FACHADA
Escala 1 : 10

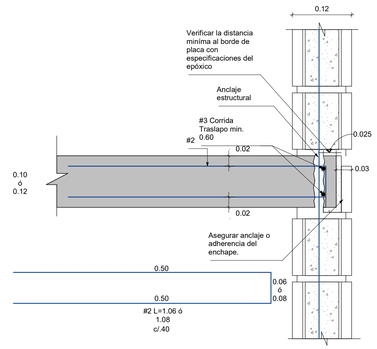

DETALLE 1 MUROS
Escala 1 : 5

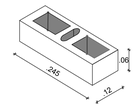

LADRILLO PRENSADO LIVIANO 6 CAPUCHINO PREHIDROFUGADO
Escala 1 : 10

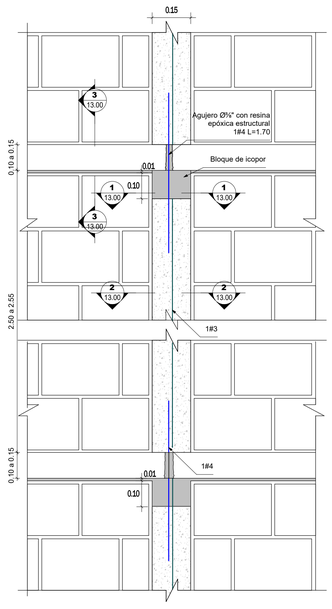

DETALLE 1 - NOES
Escala 1 : 10

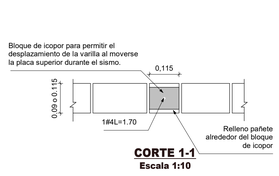

CORTE 1-1
Escala 1:10

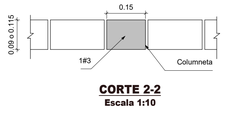

CORTE 2-2
Escala 1:10

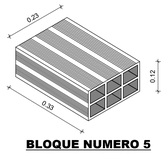

BLOQUE NUMERO 5
Escala 1 : 10

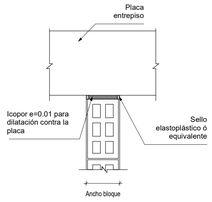

CORTE 3
Escala 1 : 10

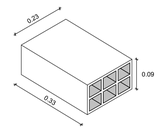

BLOQUE NUMERO 4
Escala 1 : 10

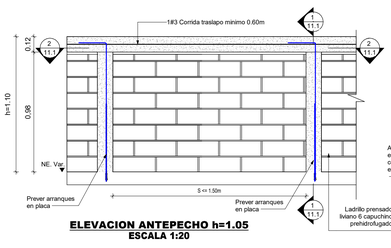

ELEVACION ANTEPECHO h=1.05
ESCALA 1:20

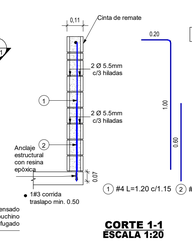

CORTE 1-1
ESCALA 1:20

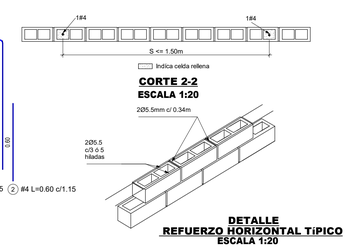

CORTE 2-2
ESCALA 1:20

DETALLE
REFUERZO HORIZONTAL TiPICO
ESCALA 1:20

NOTAS:
1. Se debe garantizar que el muro no estructural, no este vinculado a la placa superior.

ESPECIFICACIONES
f'cr (kg/cm²)
Resistencia última a la compresión del mortero de pega y mortero de relleno
100

NOTA:
Este plano debe ser revisado y aprobado por el Constructor del proyecto.

VºBº CONSTRUCTOR

Grado de desempeño: **Bajo**
Grupo de uso: **1**
Coeficiente de importancia:
I=1.0

VERSIÓN : 1

PLANO Nº 13.00

Aycardi Estructural

GERENTE DE PROYECTO
ROBERTO AYCARDI F.
MAT. 2520257258 CND

INGENIERO
CARLOS ANDRÉS WILCHES C.

MODELADOR
DANIEL CASTELLANOS

MODIFICACIONES	FECHA
Emisión Inicial	28-02-2025

MARVAL

LA SCALA

LA SCALA_EST_TOR-1

TORRE 1

CALLE 170 CON AV. BOYACA

DETALLES NOES

LA SCALA_EST_TOR-1 _13.00_DT-NOES

REVISOR ESTRUCTURAL
RAMÓN ÁNDRES ALVAREZ MANTILLA
MAT. 25202-346546 CND.

PLANO Nº 13.00 VERSIÓN : 1